

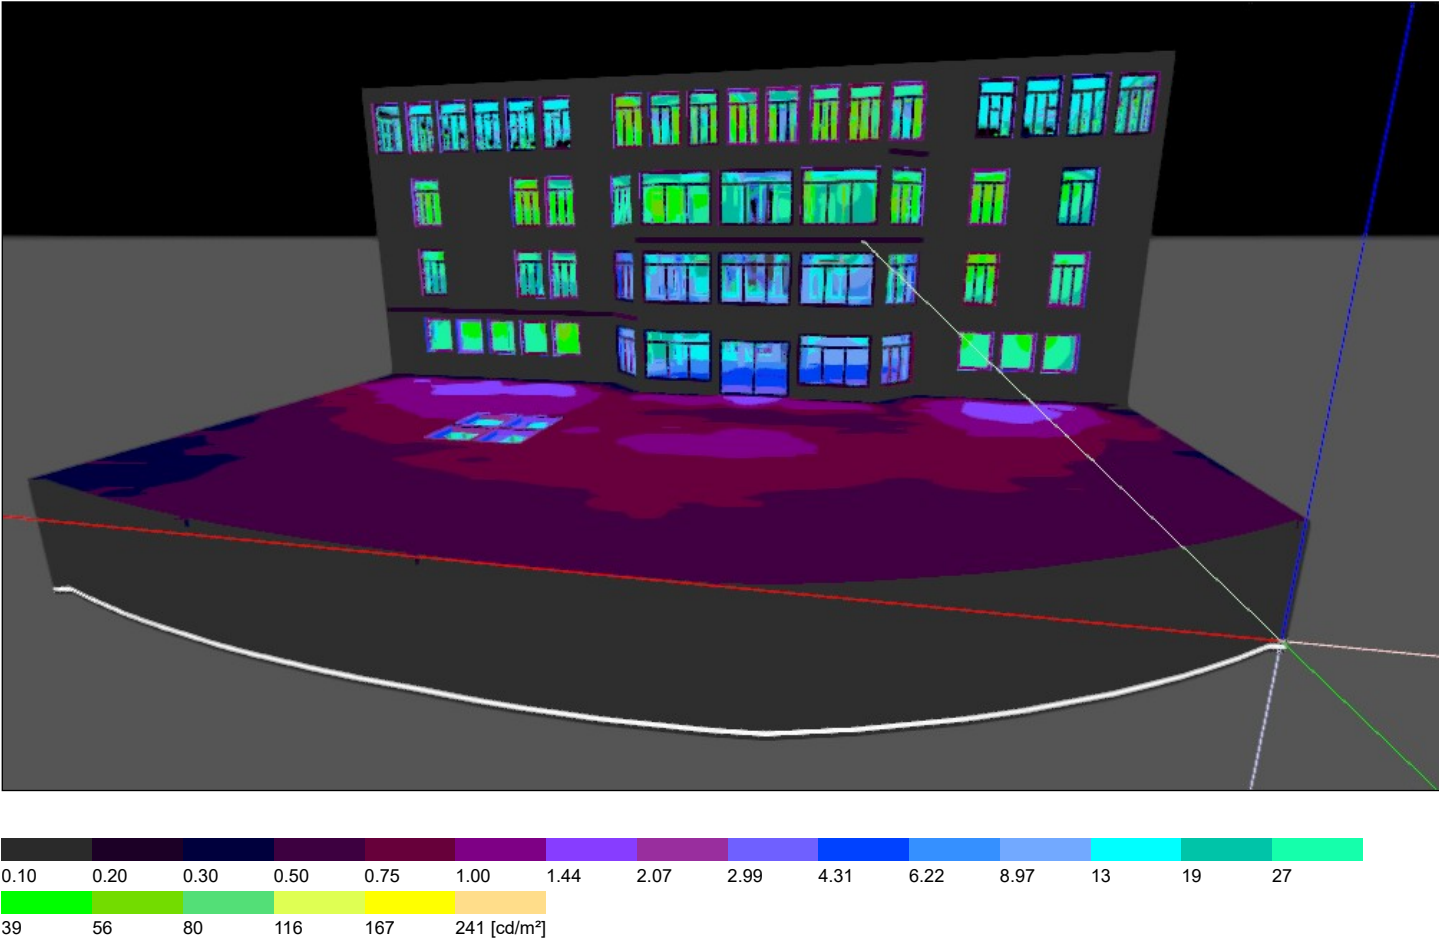


Room 2


Building 2, Luminance values in [cd/m²]

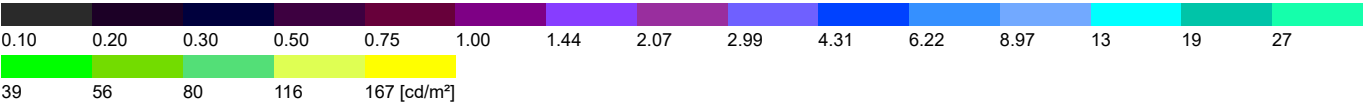


Building 2 (opp), Luminance values in [cd/m²]

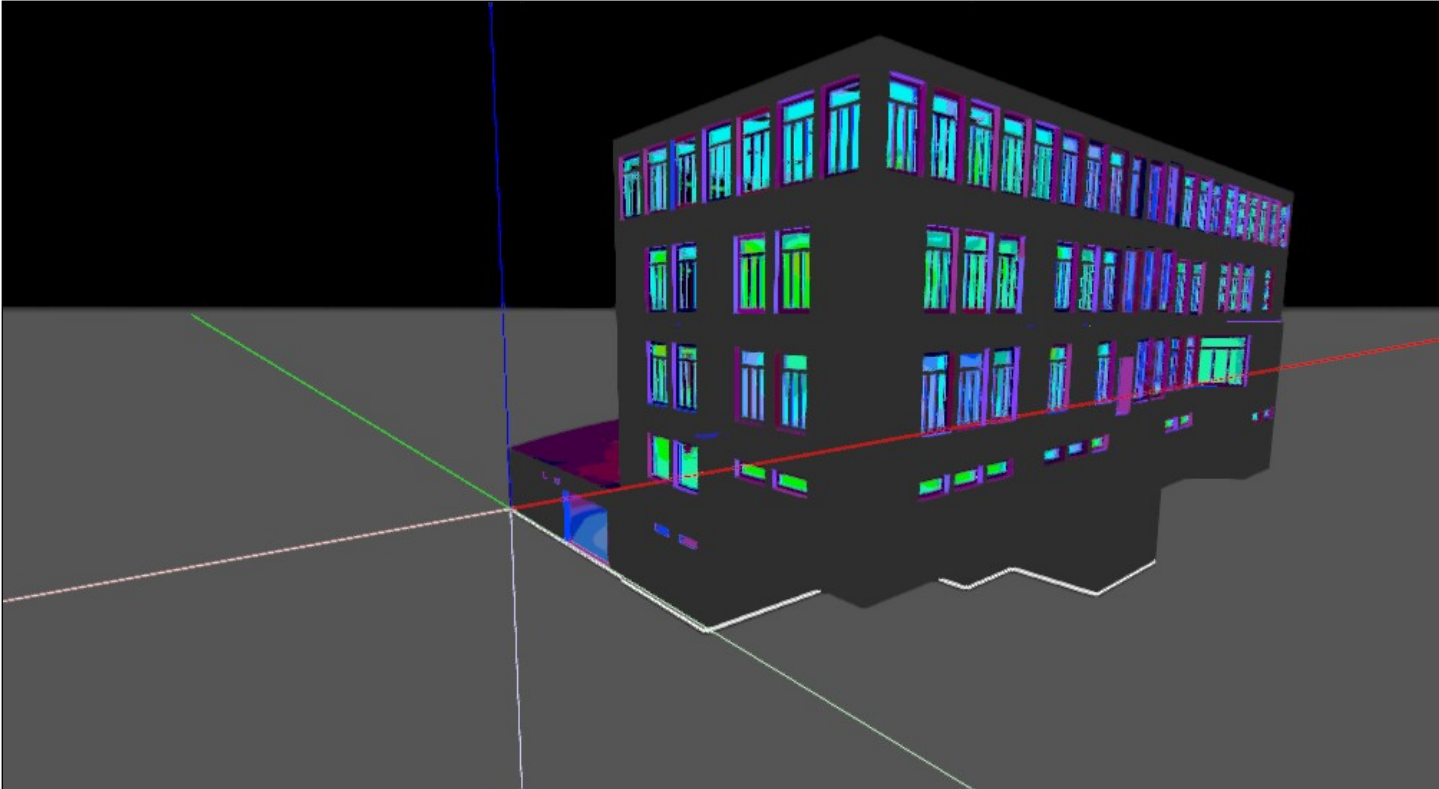


basement, Luminance values in [cd/m²]

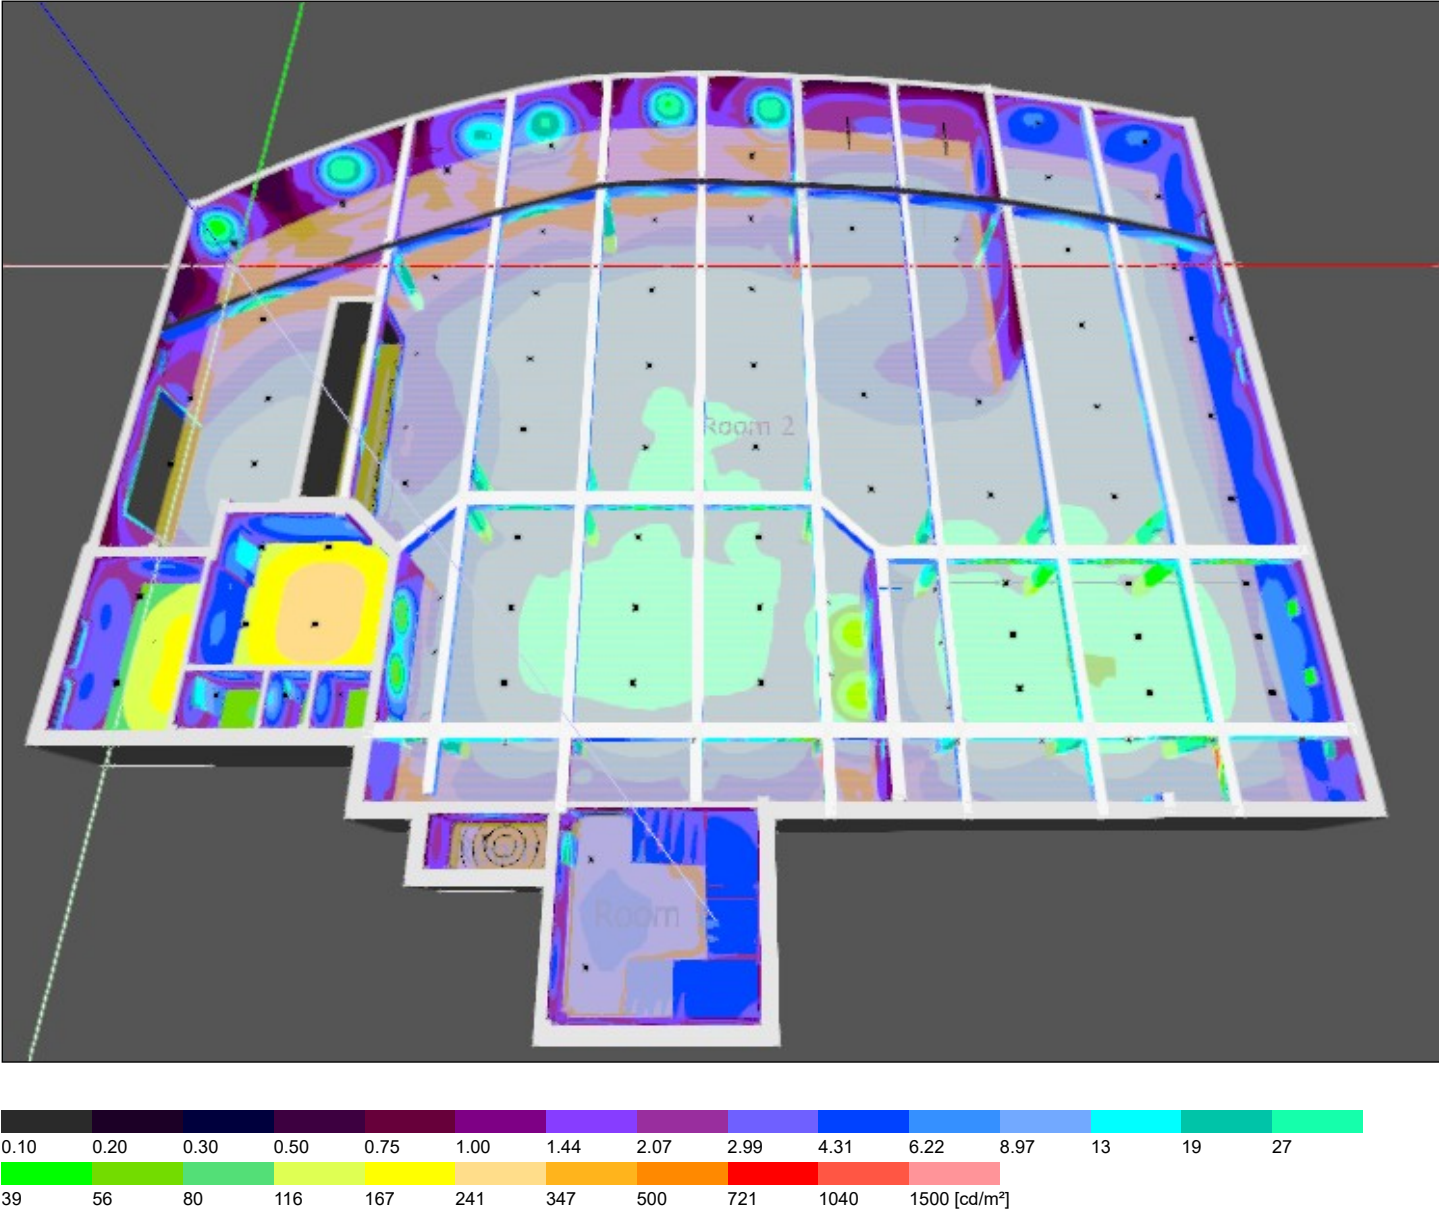


ground floor, Luminance values in [cd/m²]

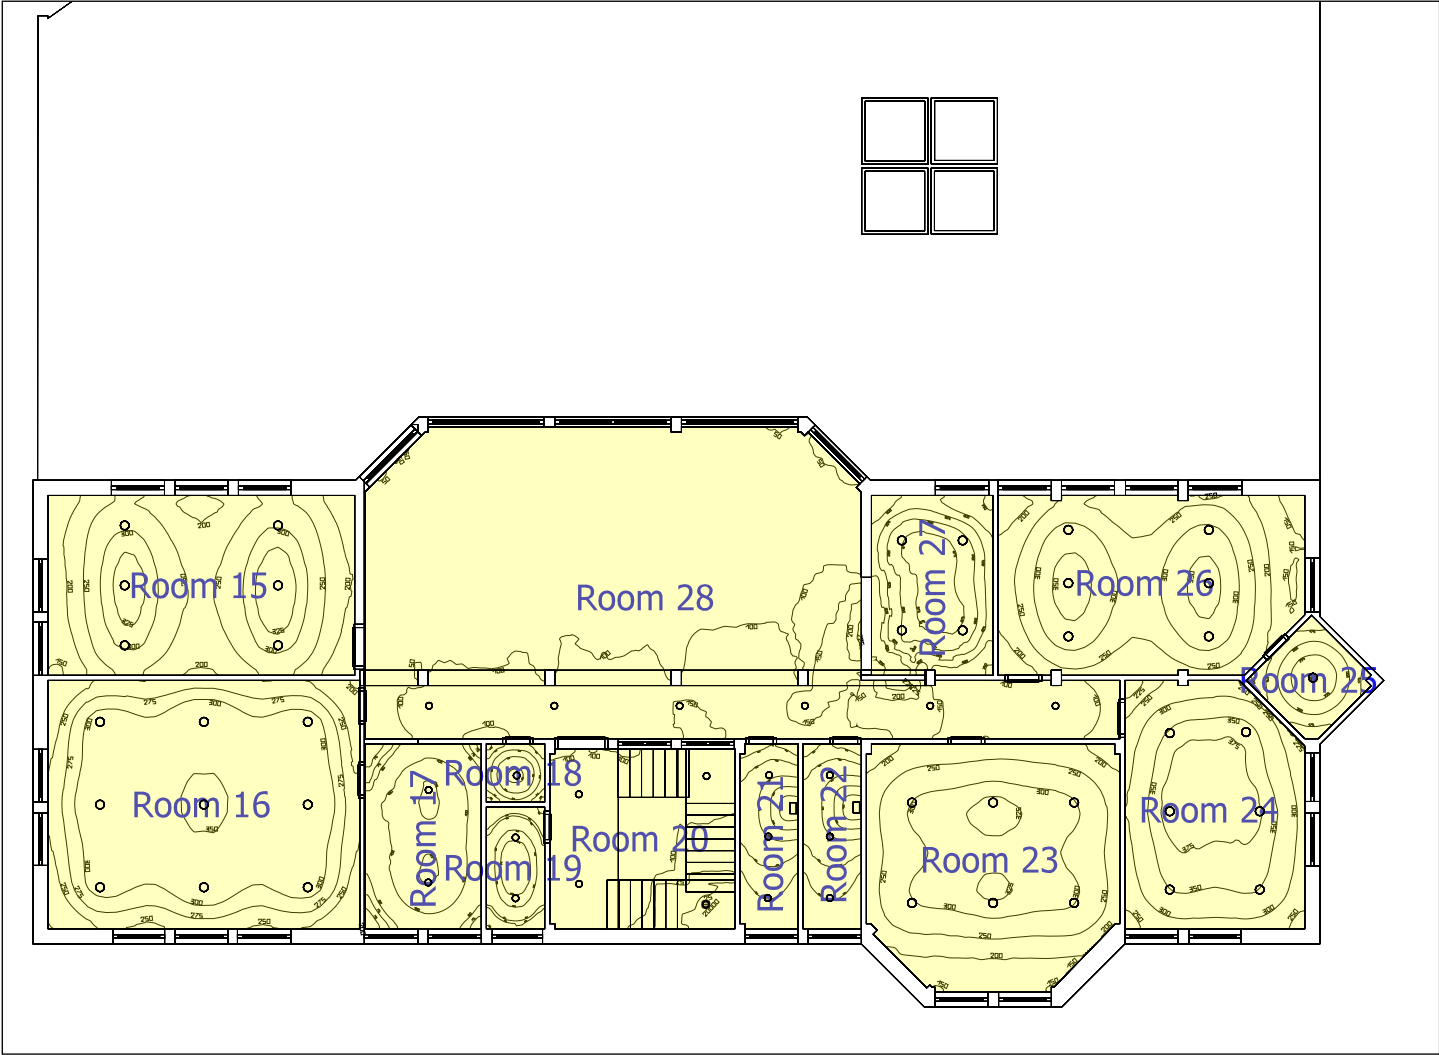


Scale: 1 : 179

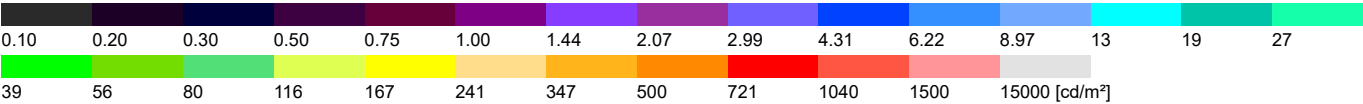


ground floor (3D), Luminance values in [cd/m²]

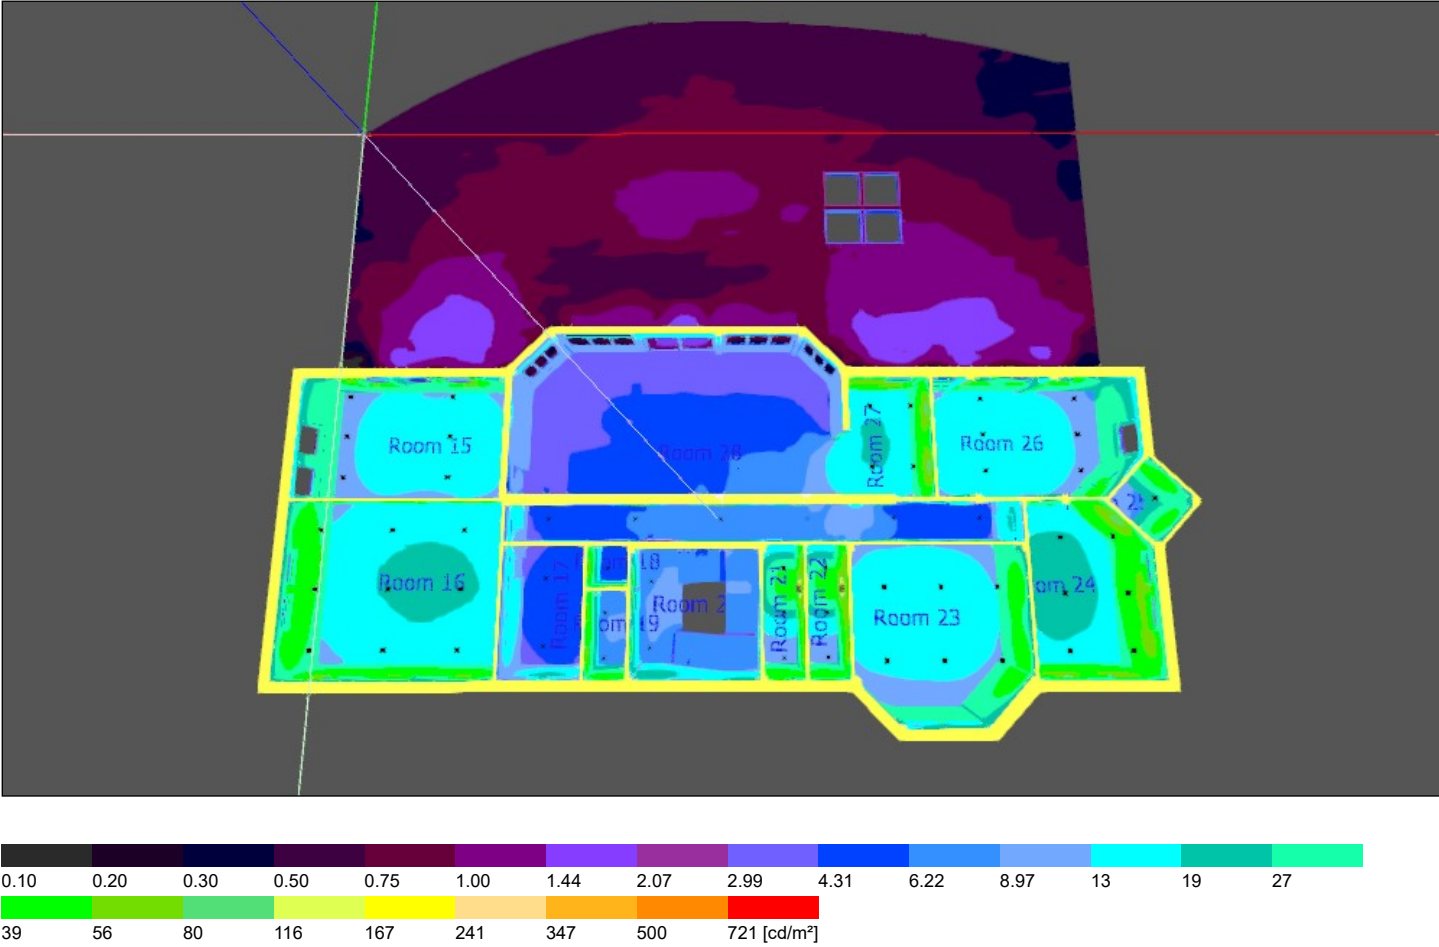


1st floor, Luminance values in [cd/m²]

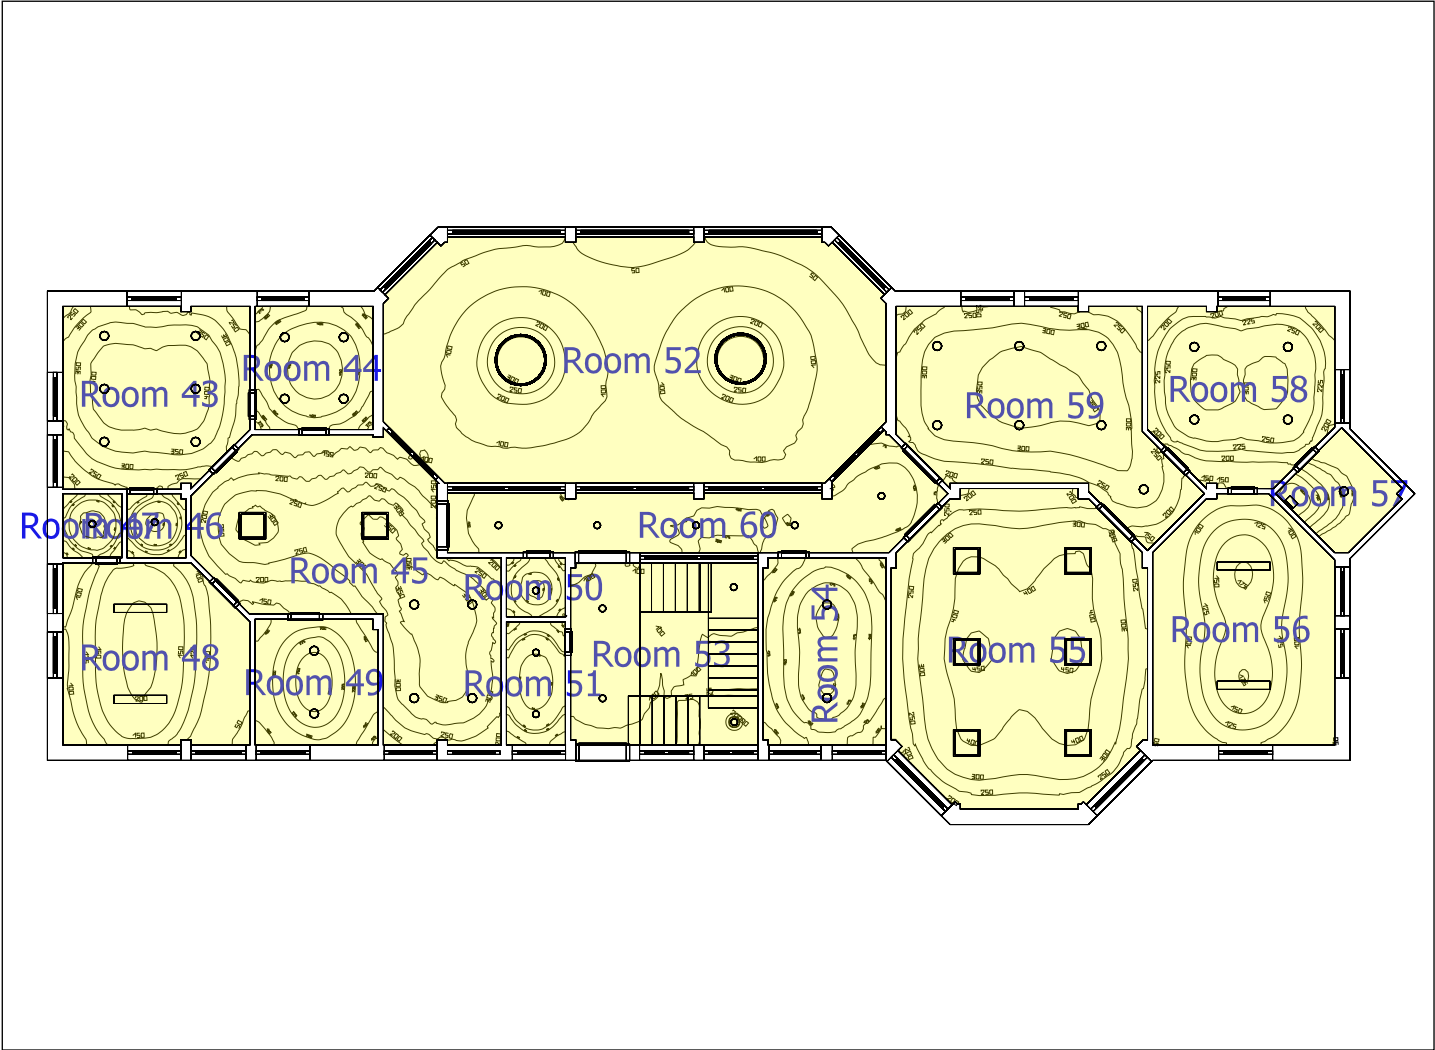


Scale: 1 : 177

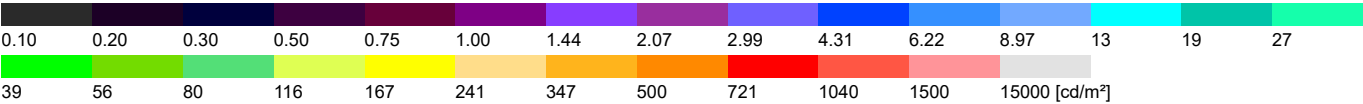


1st floor (3D), Luminance values in [cd/m²]

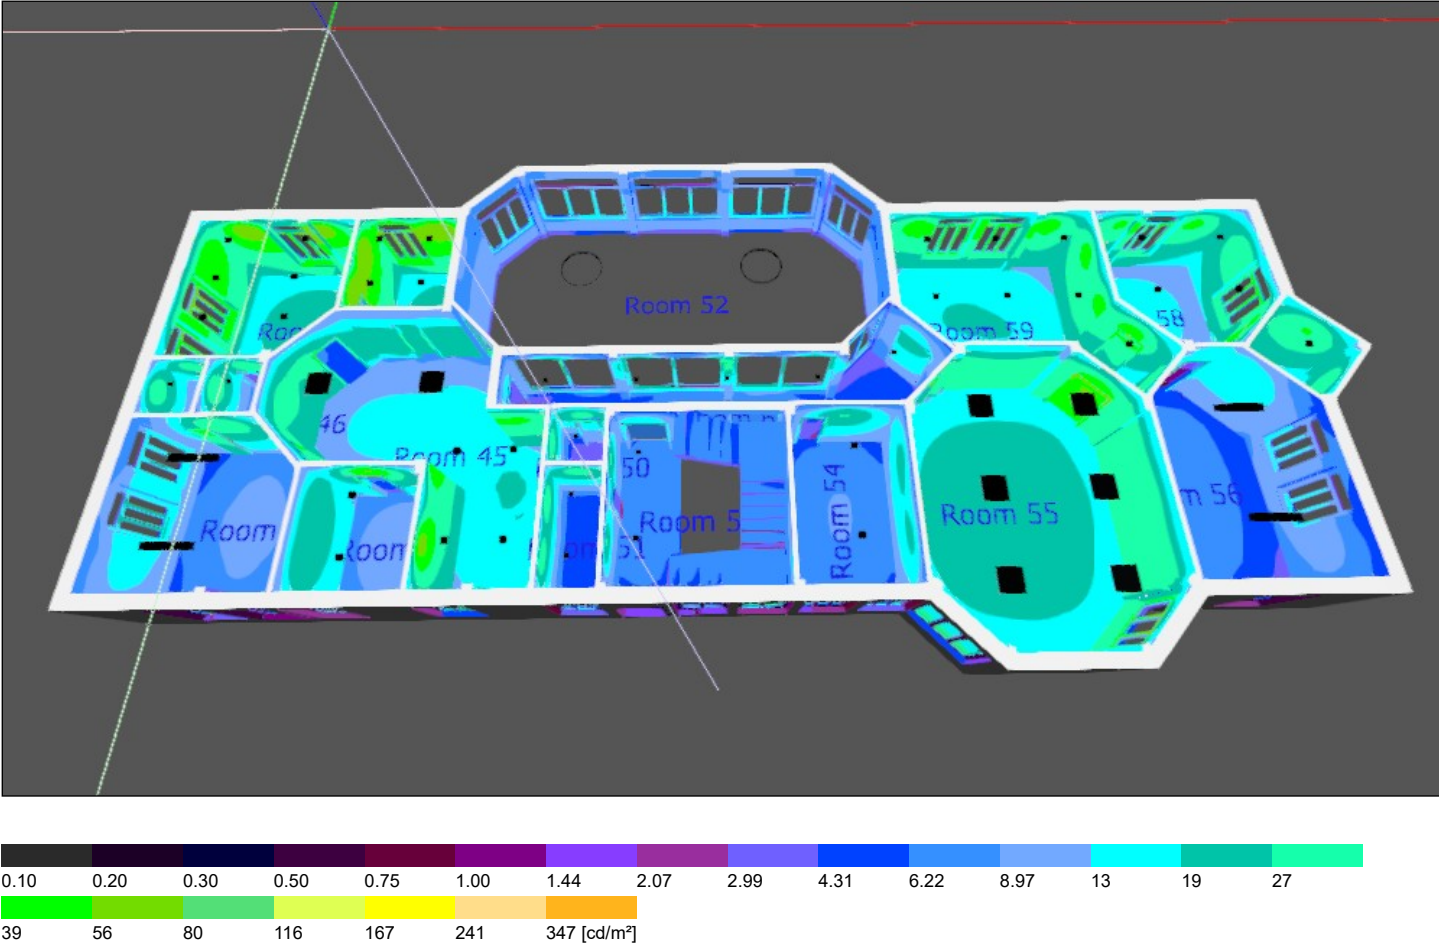



2nd floor, Luminance values in [cd/m²]

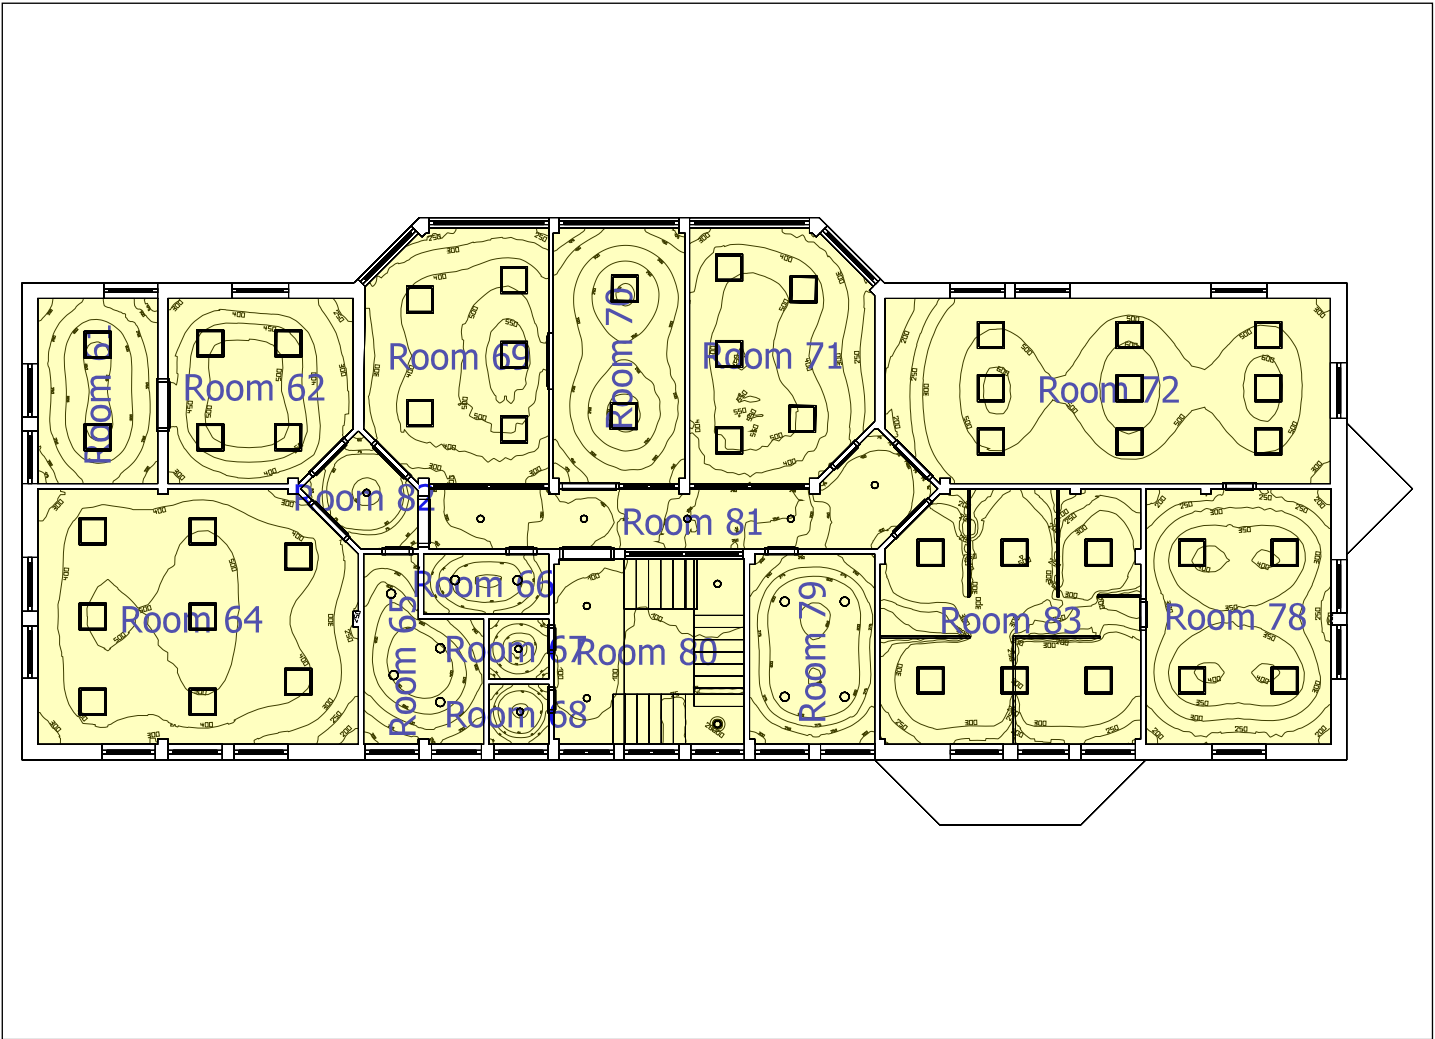


Scale: 1 : 174

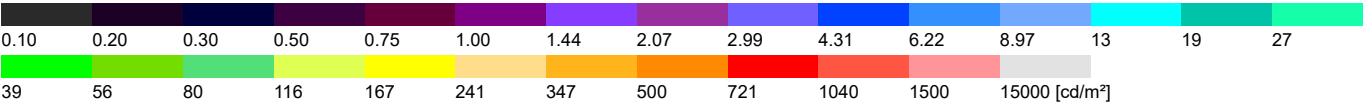


2nd floor (3D), Luminance values in [cd/m²]

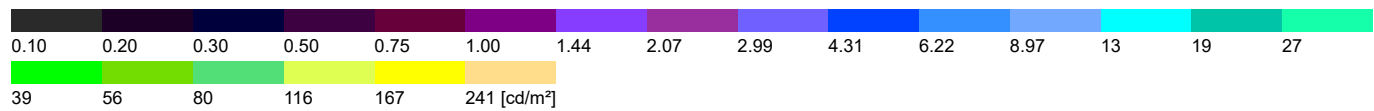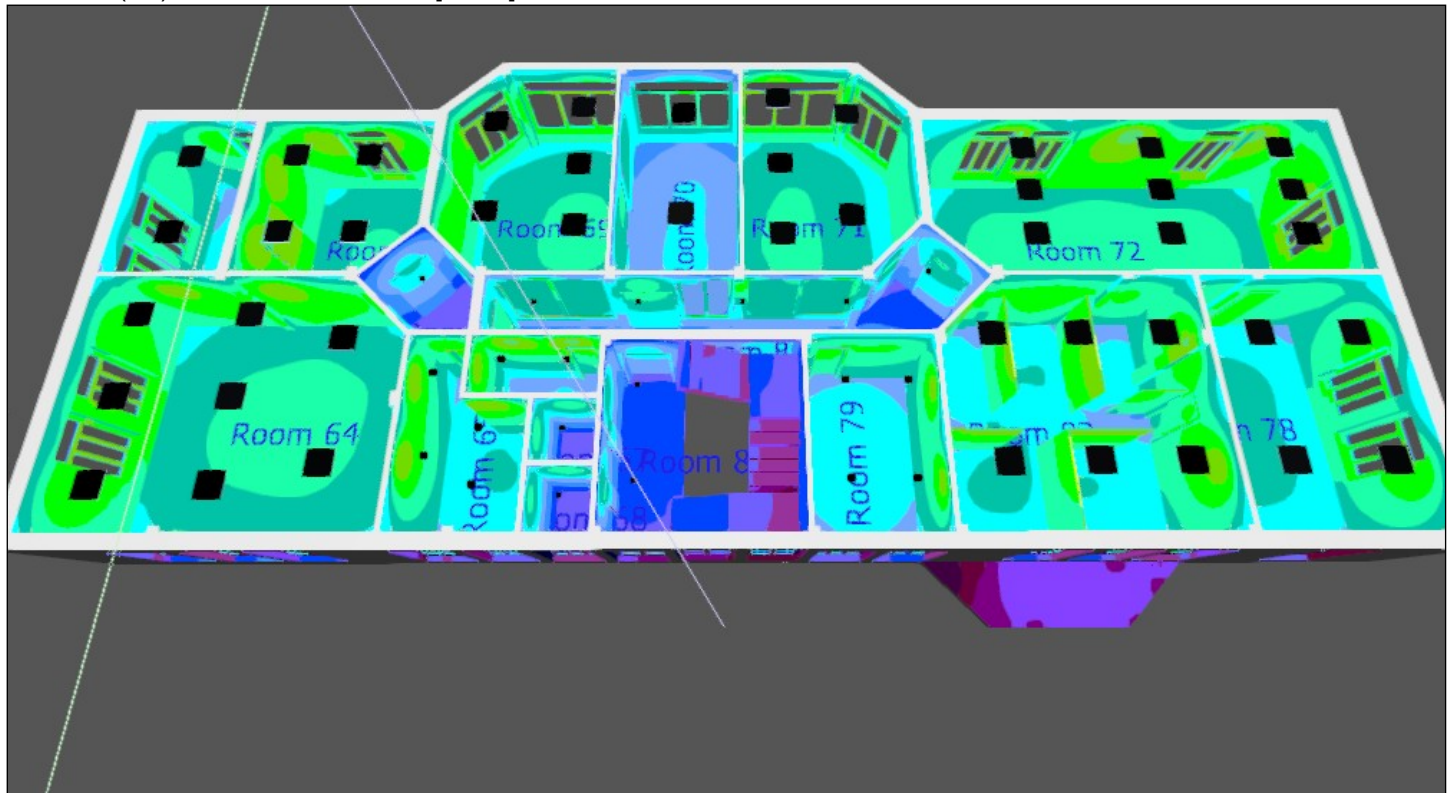


3rd floor, Luminance values in [cd/m²]

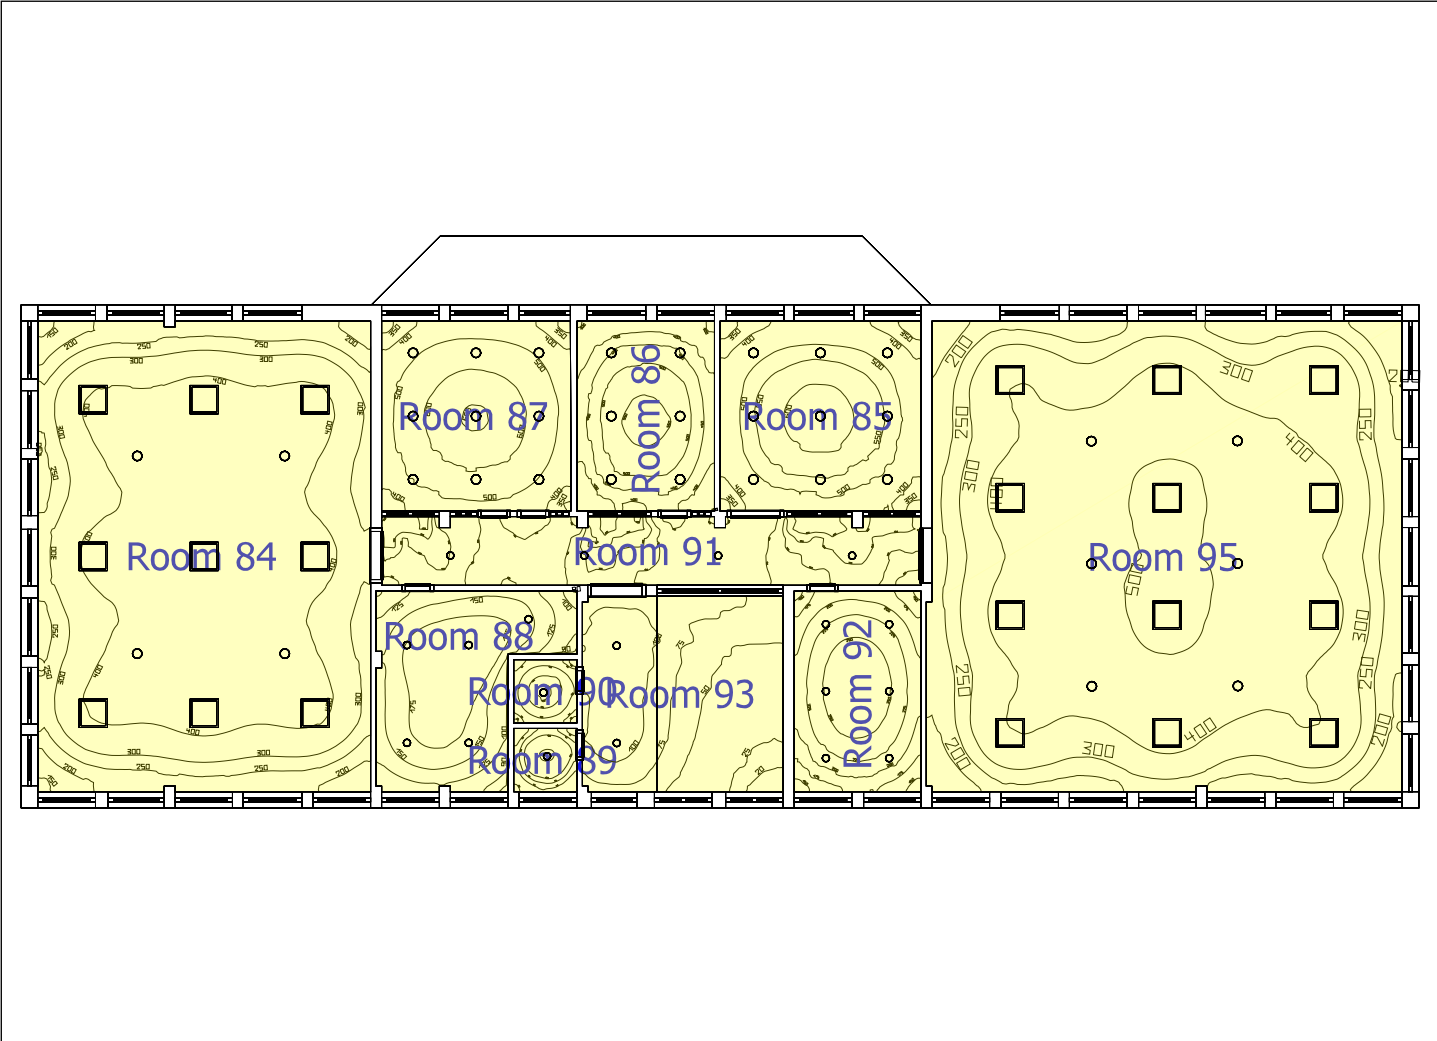

Scale: 1 : 165

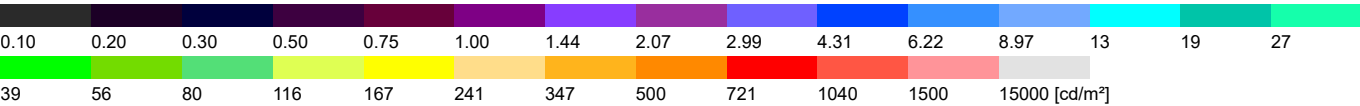


3rd floor (3D), Luminance values in [cd/m²]


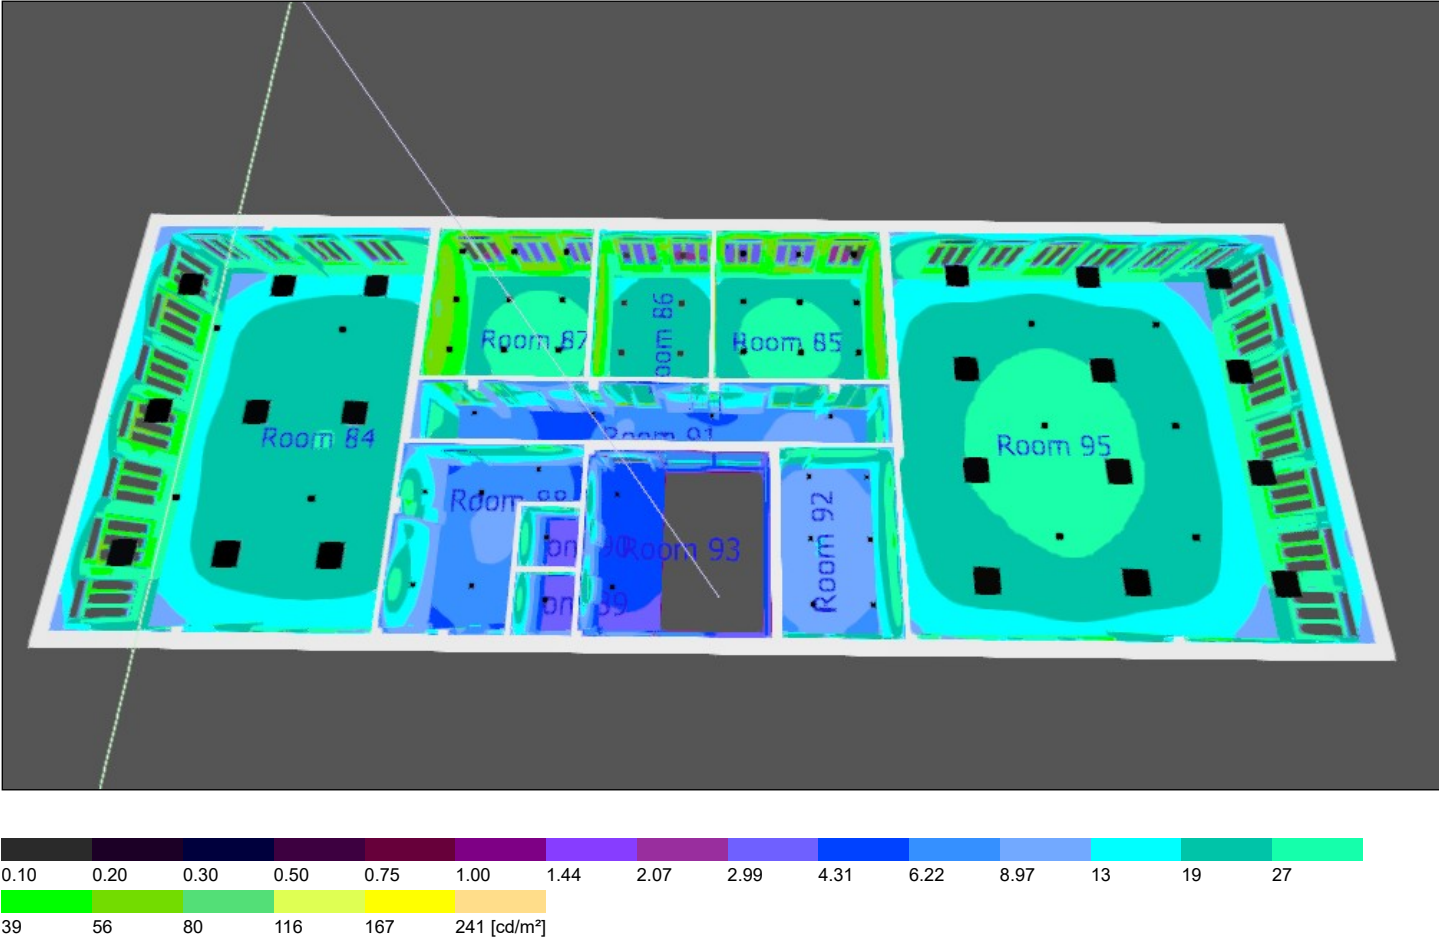


Room 1



Building 1, Illuminance values in [lx]

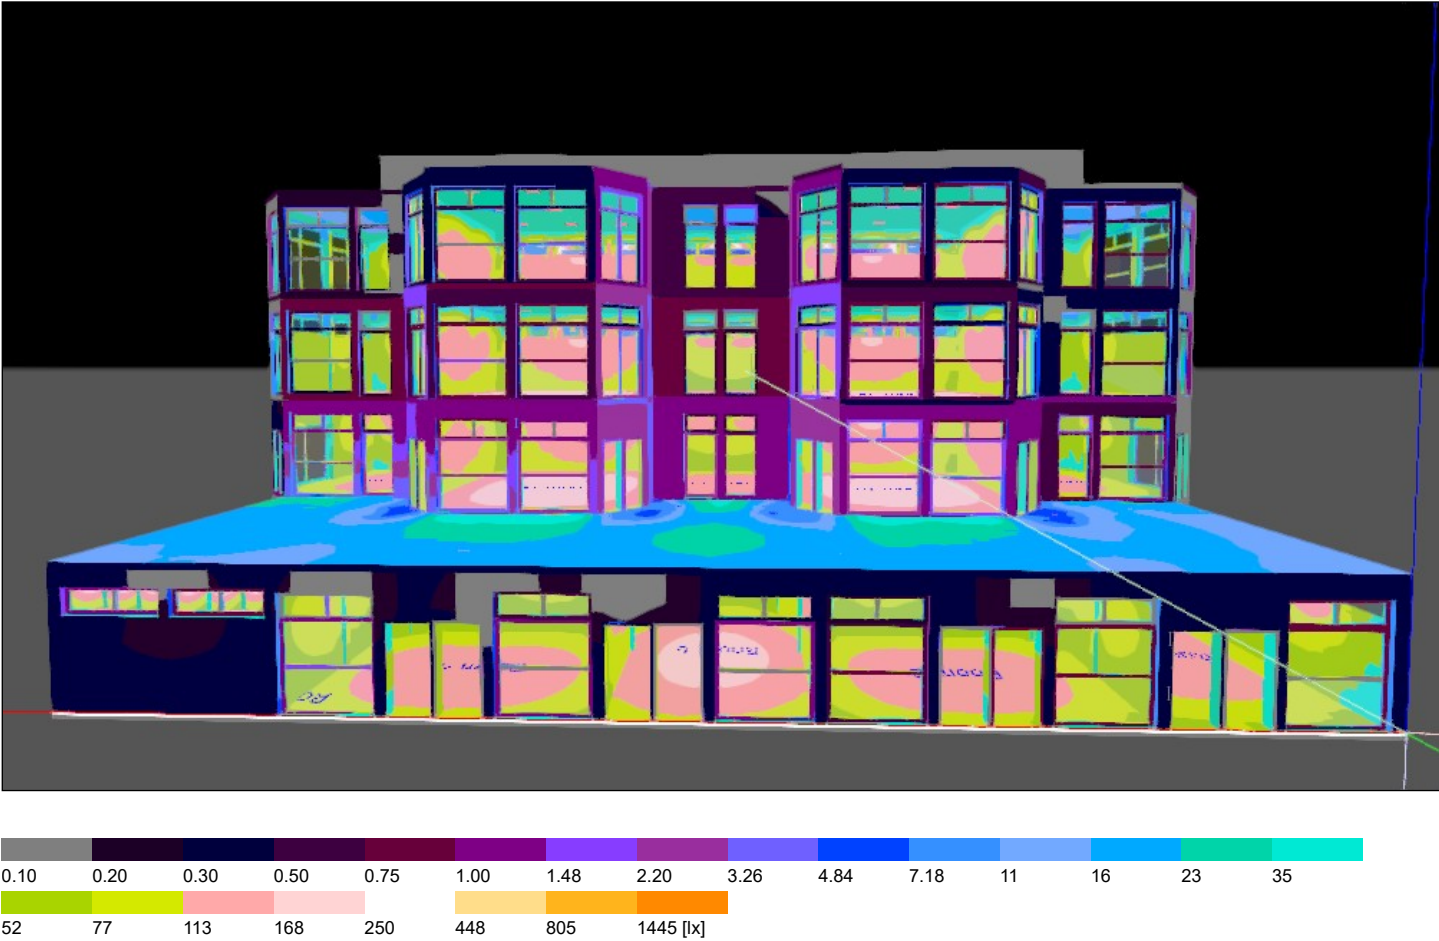


Building 1 (2), Illuminance values in [lx]

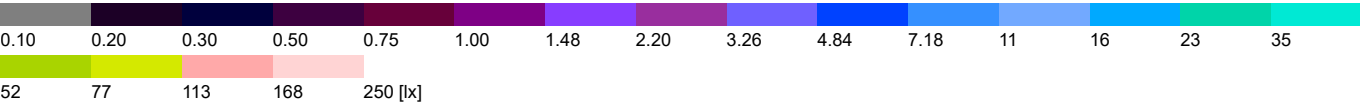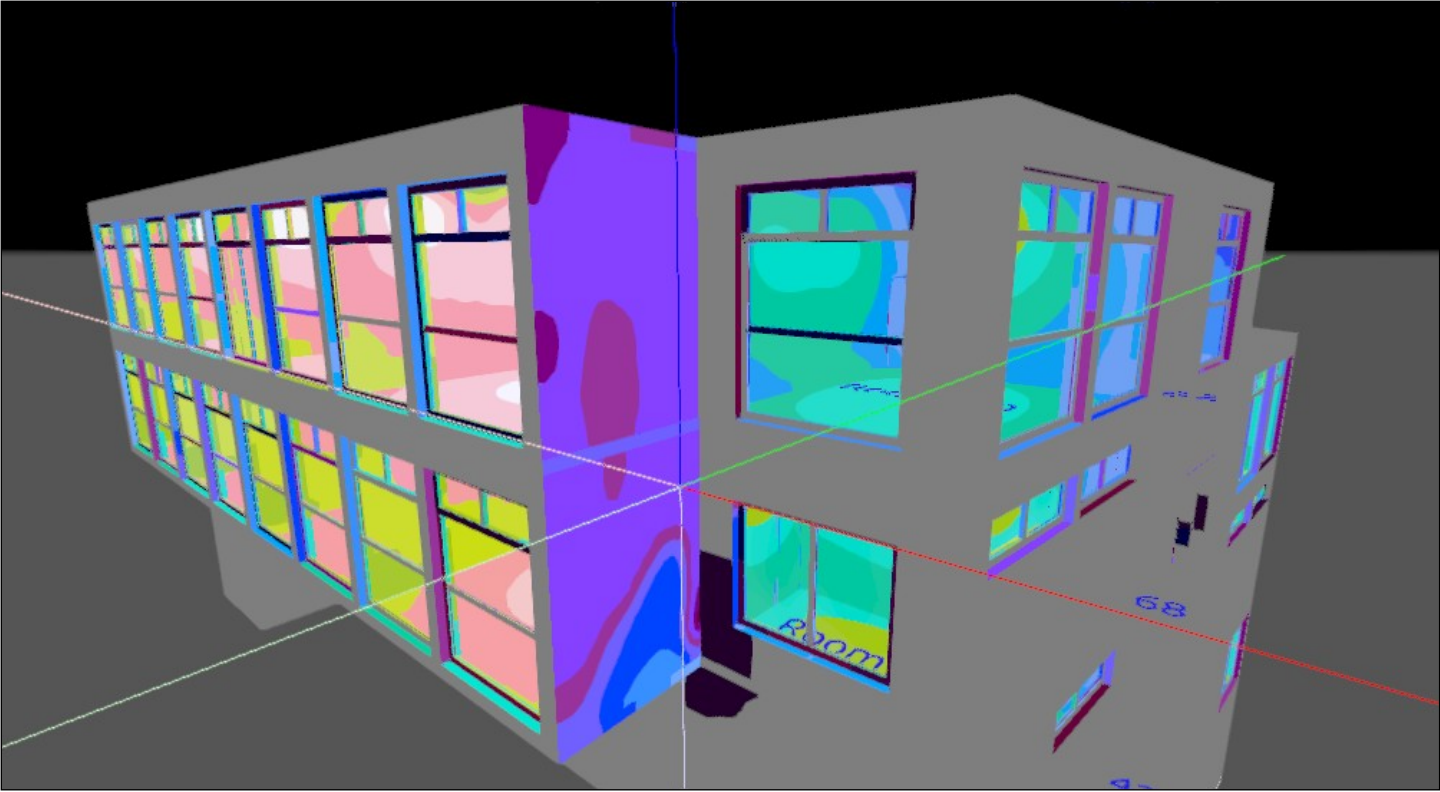


Storey 1 (3D), Illuminance values in [lx]

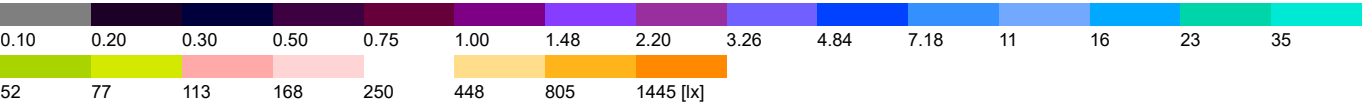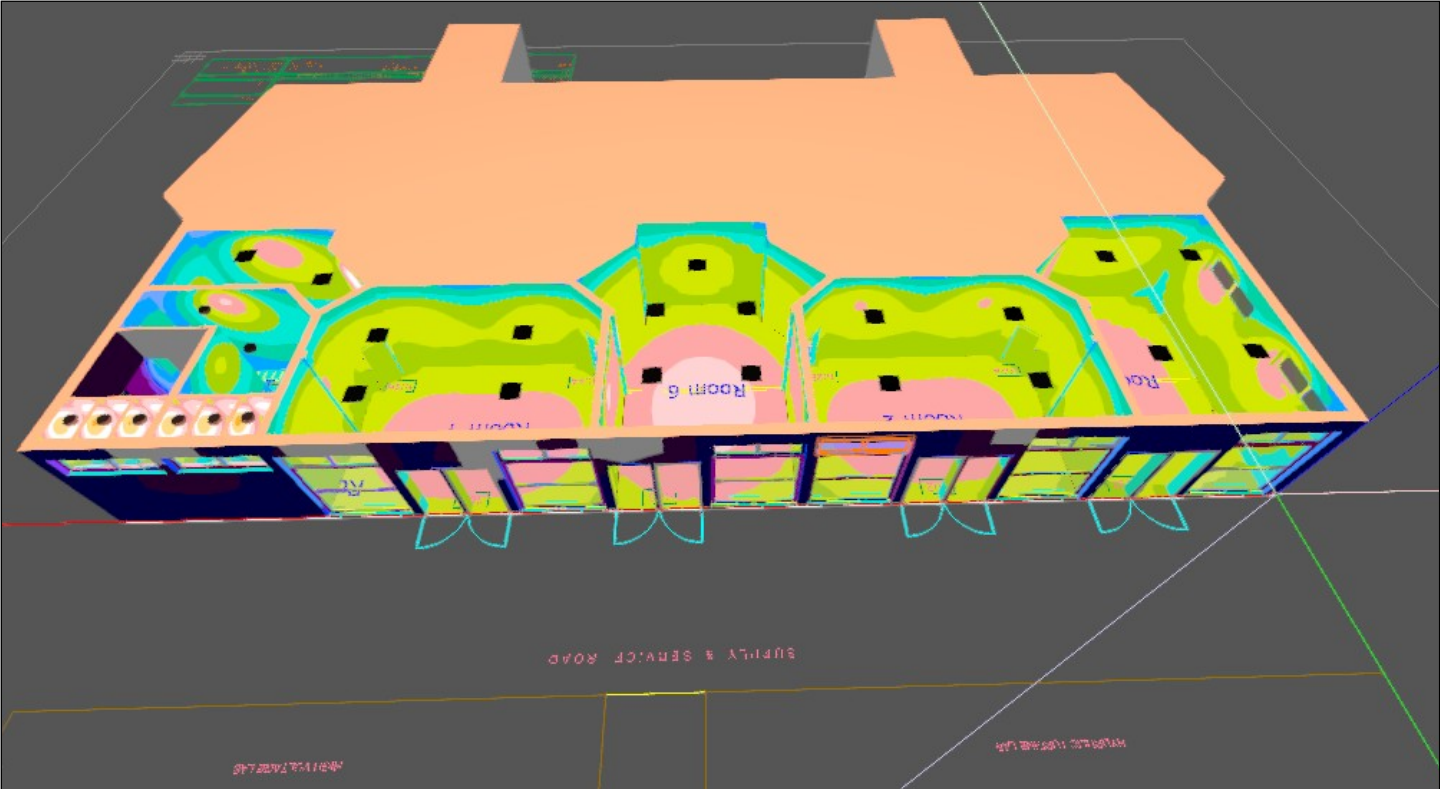



Storey 1, Illuminance values in [lx]

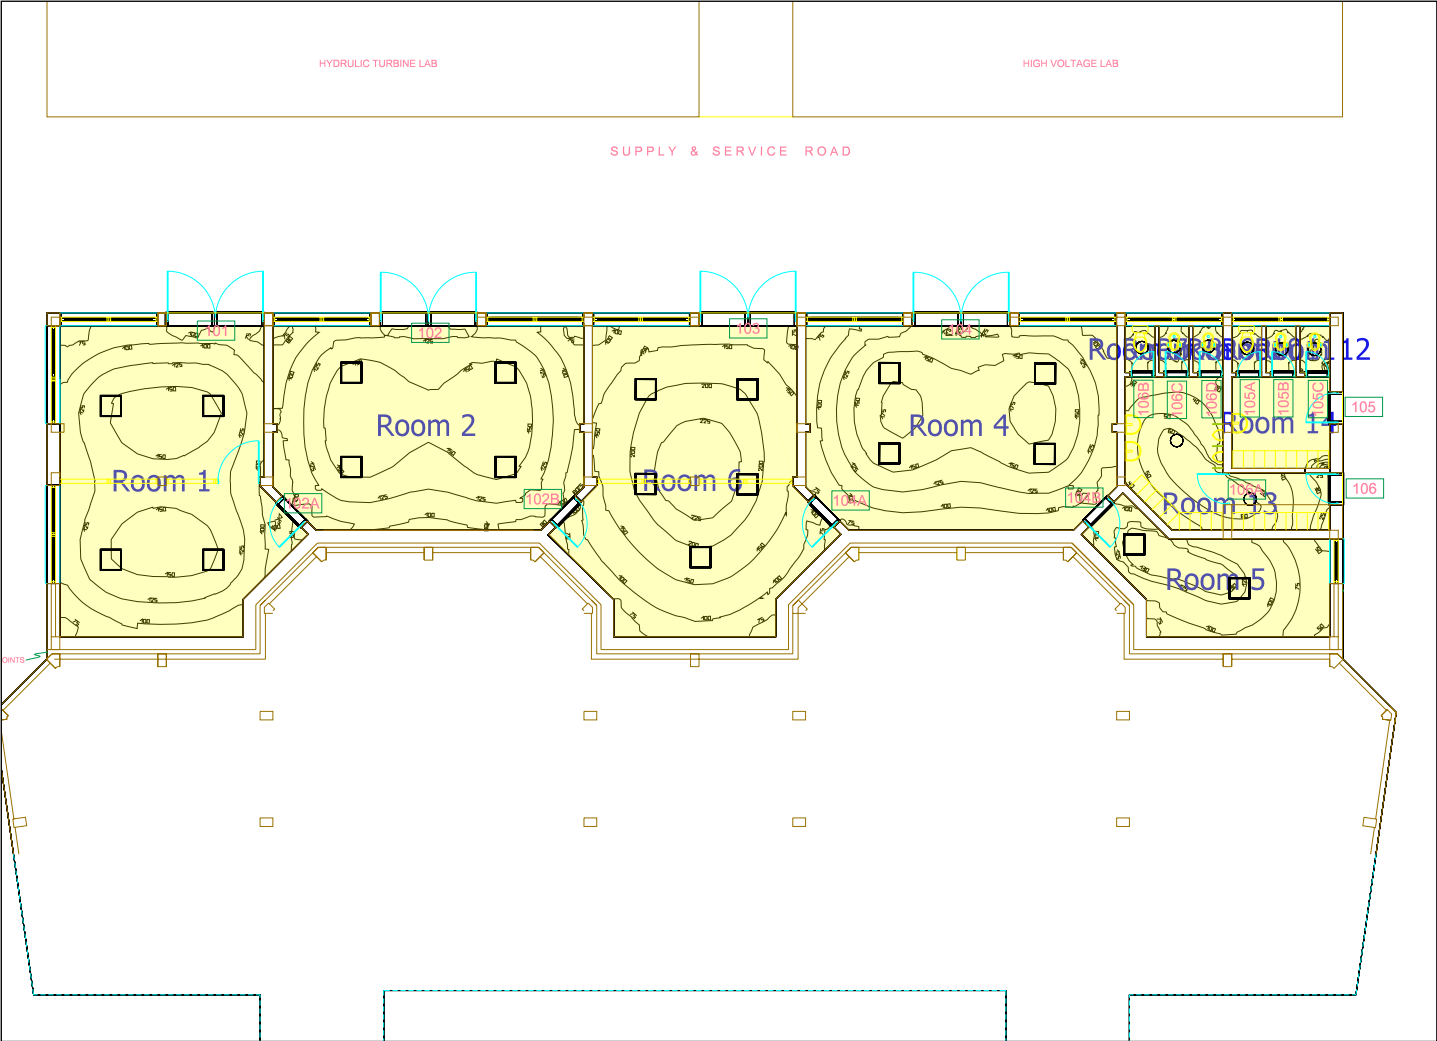


Scale: 1 : 213

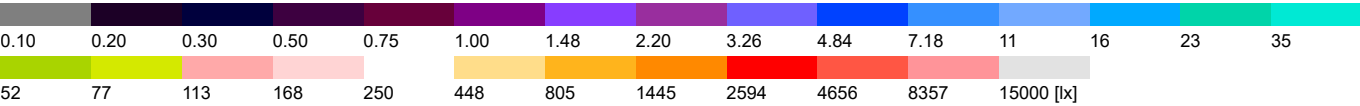


Storey 2 (3D), Illuminance values in [lx]

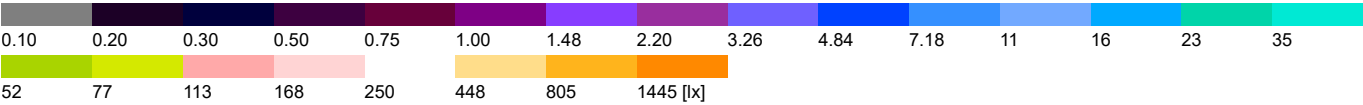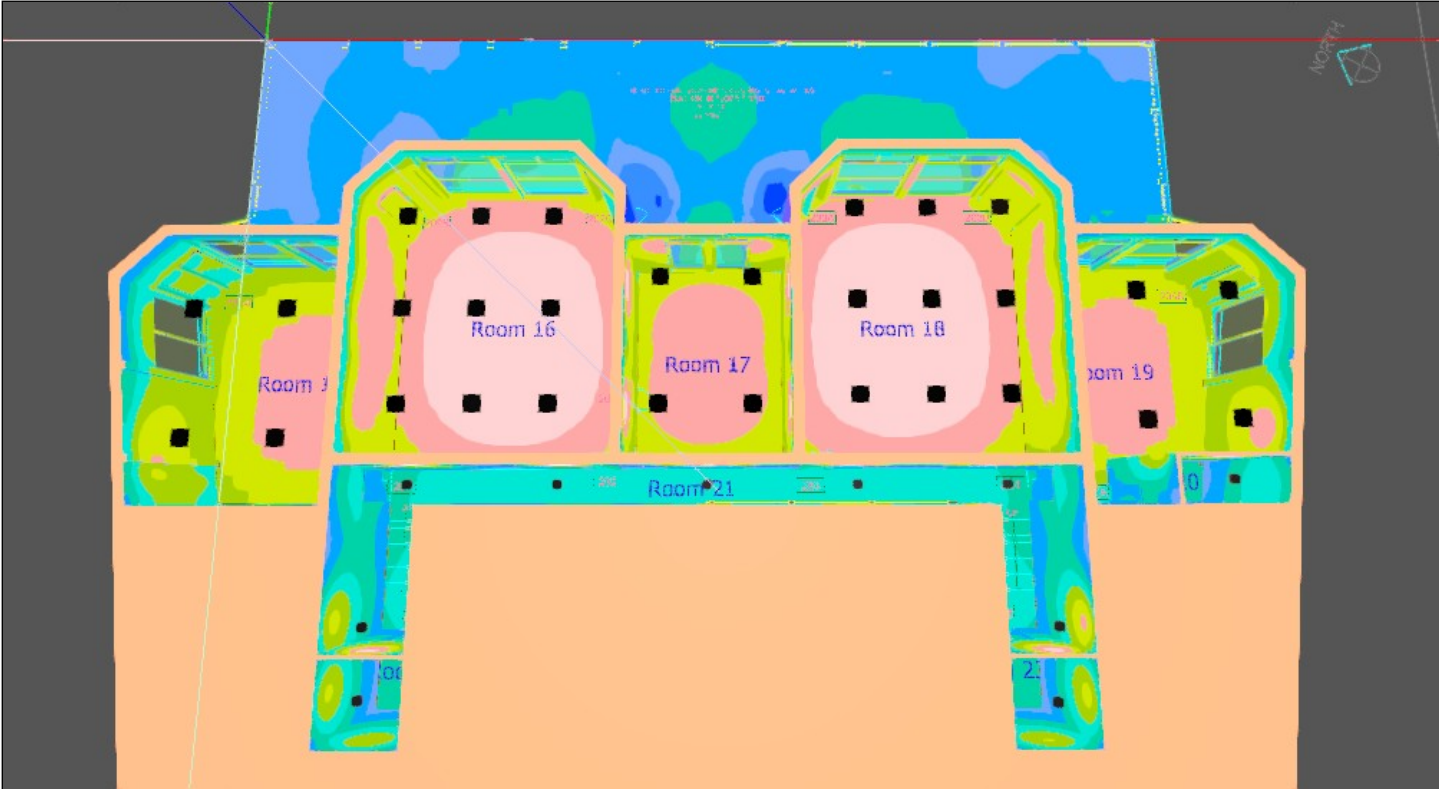


Storey 2, Illuminance values in [lx]

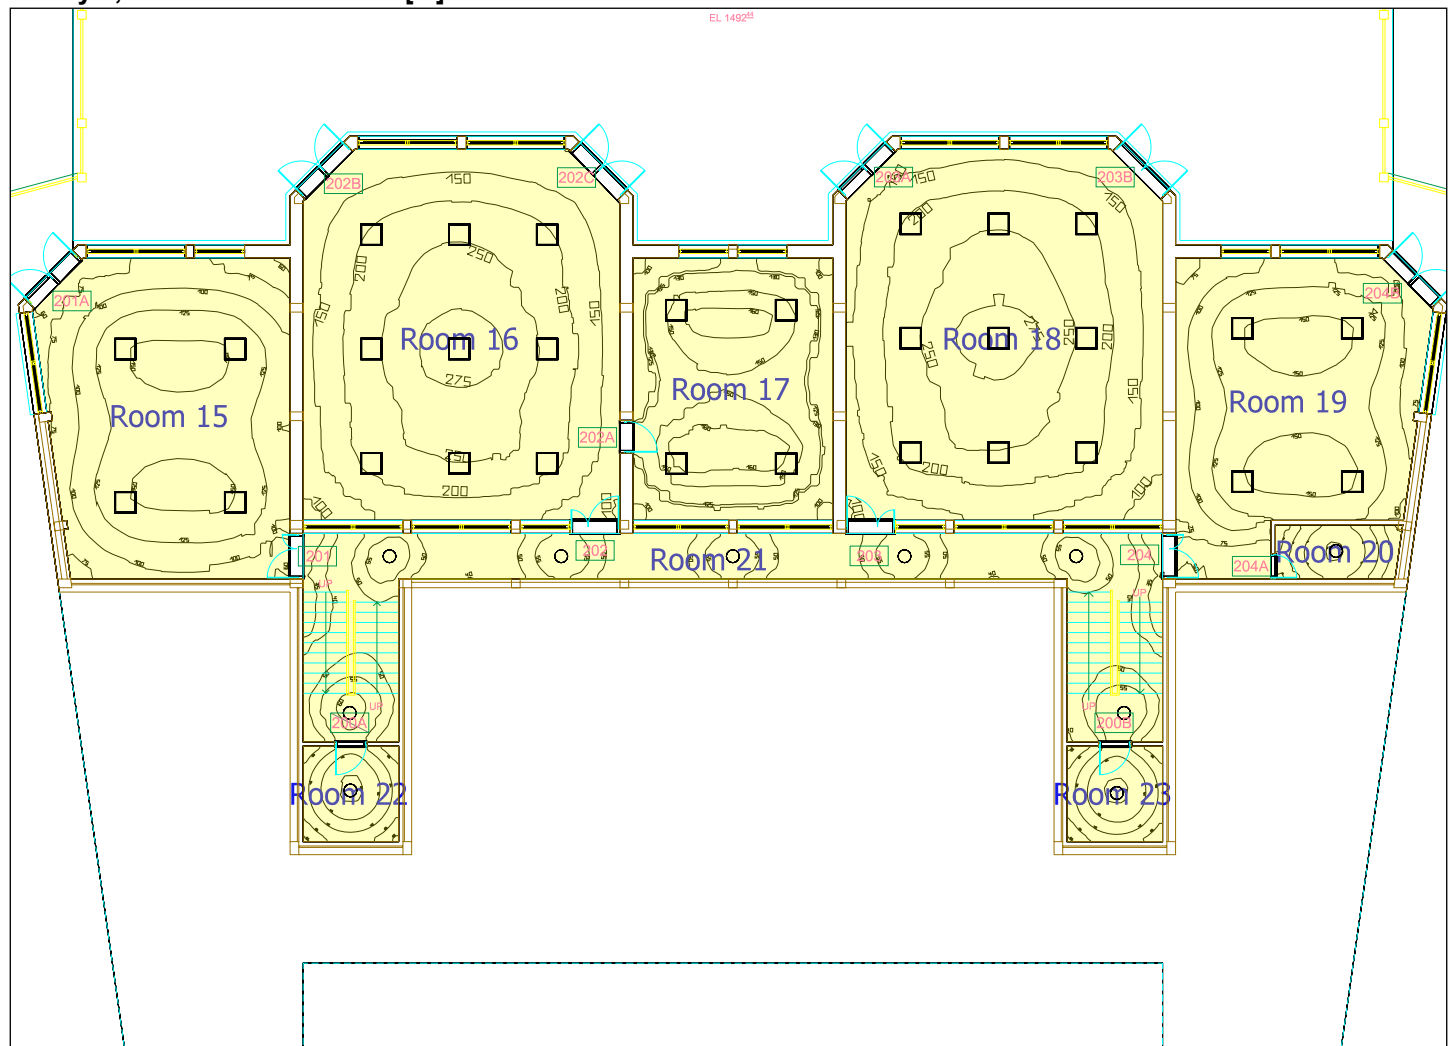


Scale: 1 : 209

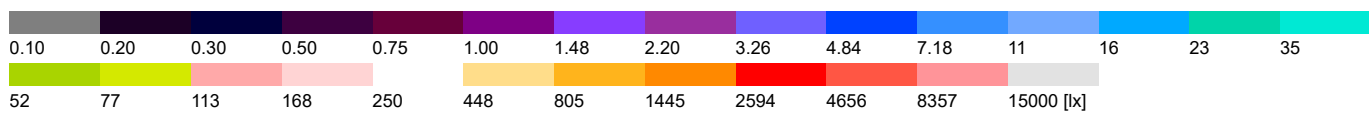


Storey 3(3D), Illuminance values in [lx]

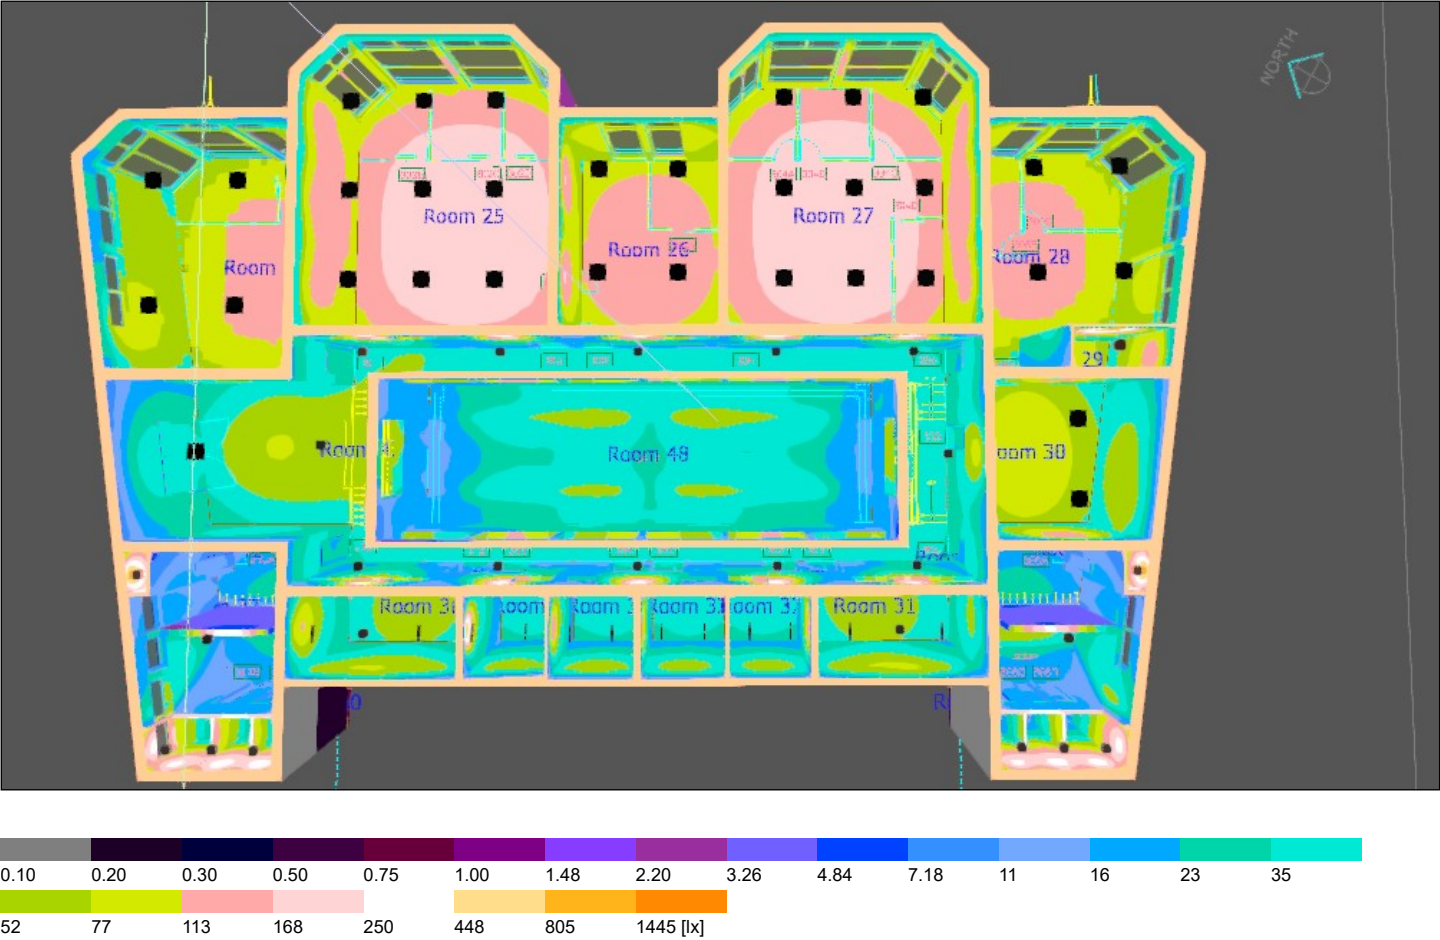


Storey 3, Illuminance values in [lx]

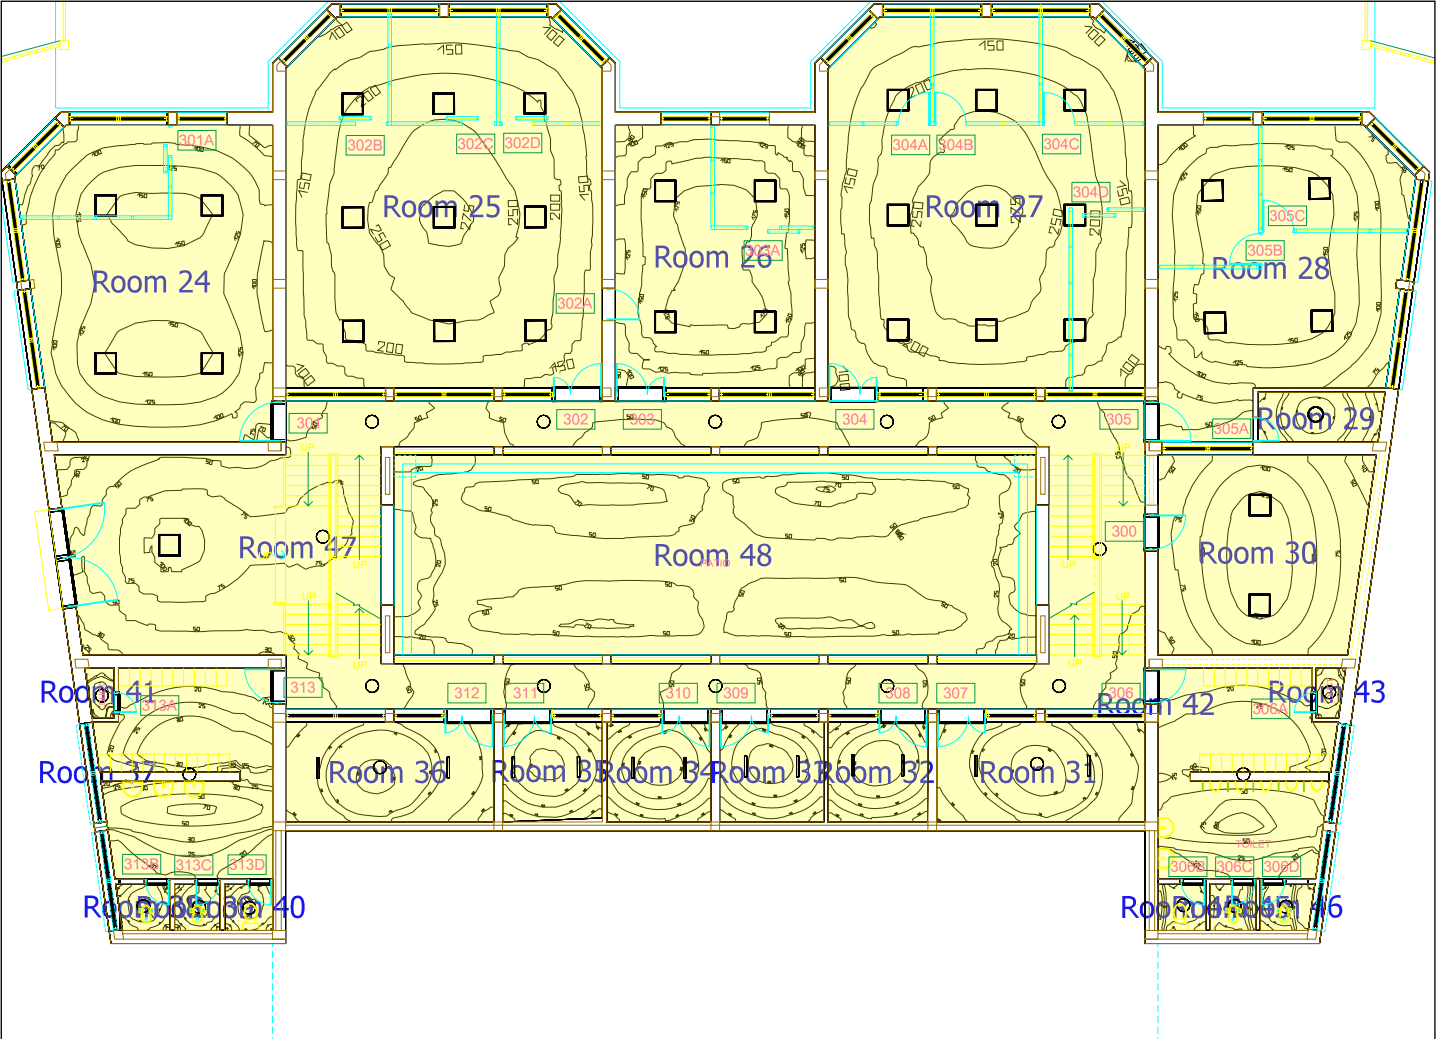


Scale: 1 : 209

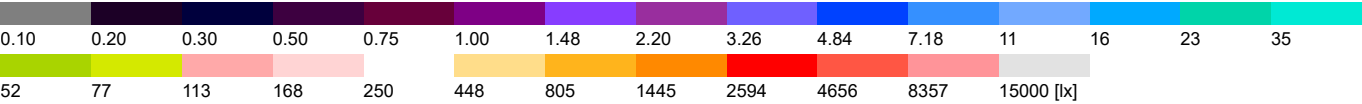


Storey 4 (3D), Illuminance values in [lx]

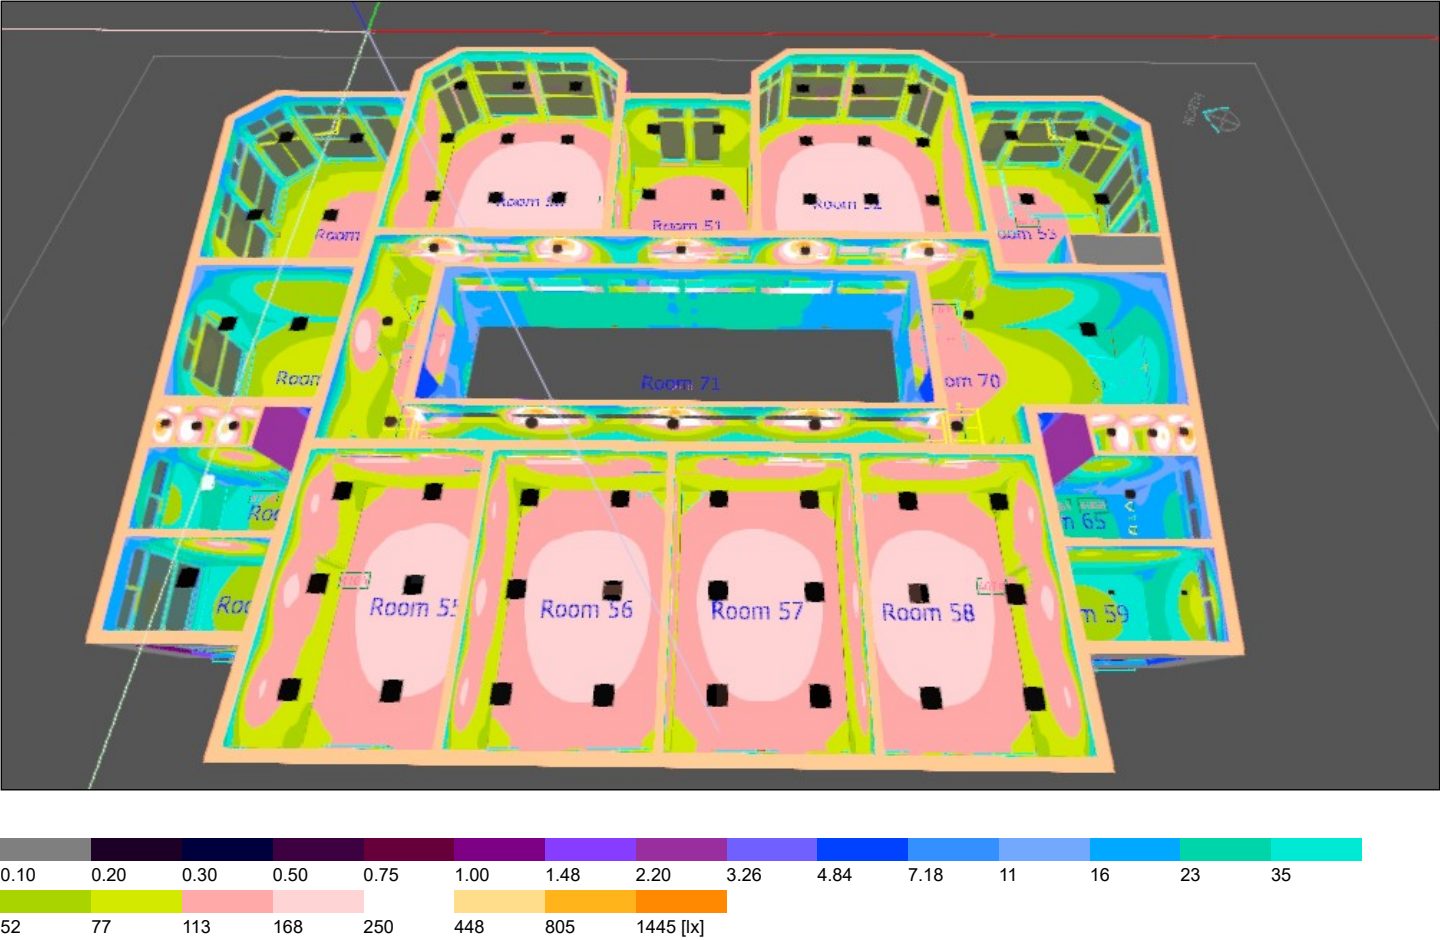



Storey 4, Illuminance values in [lx]

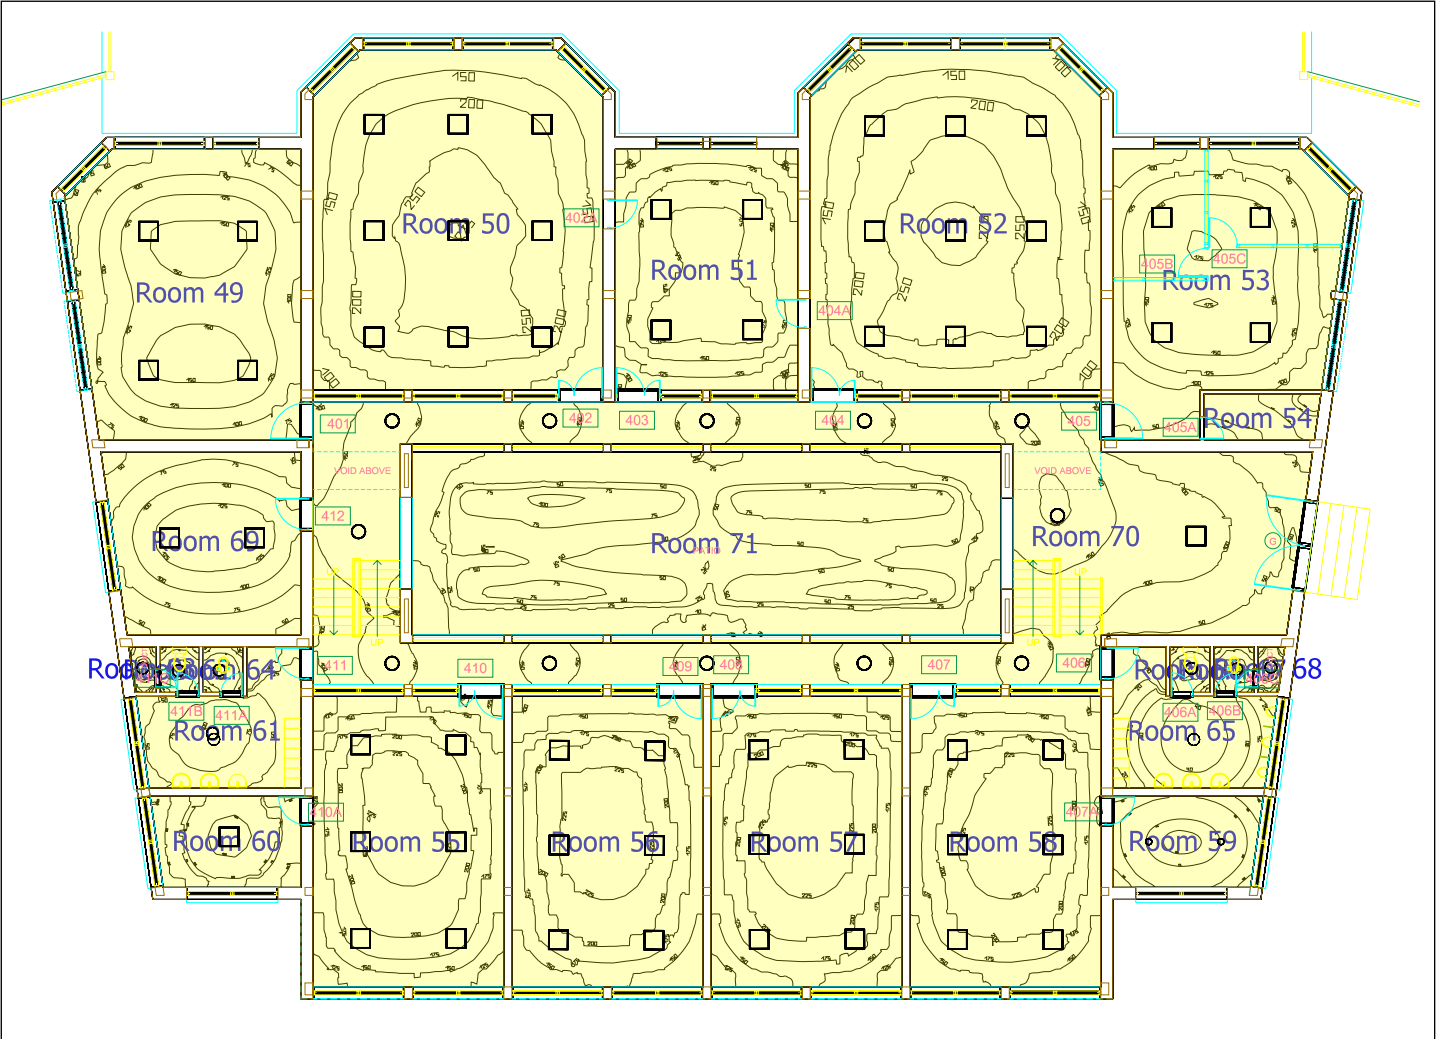


Scale: 1 : 228

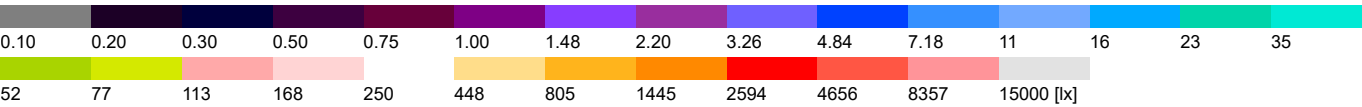


Storey 5 (3D), Illuminance values in [lx]

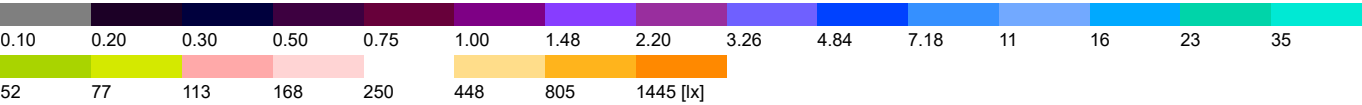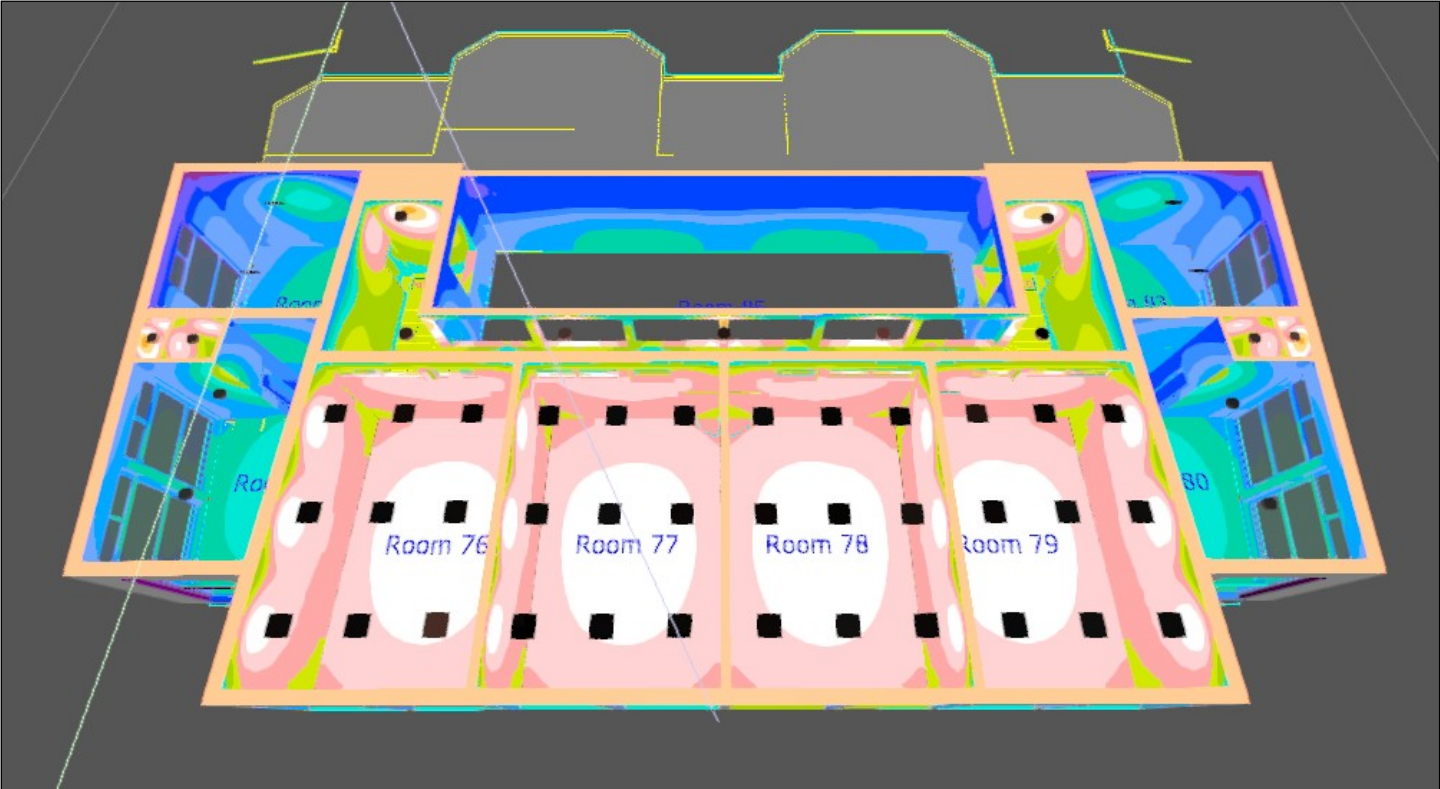

Storey 5, Illuminance values in [lx]

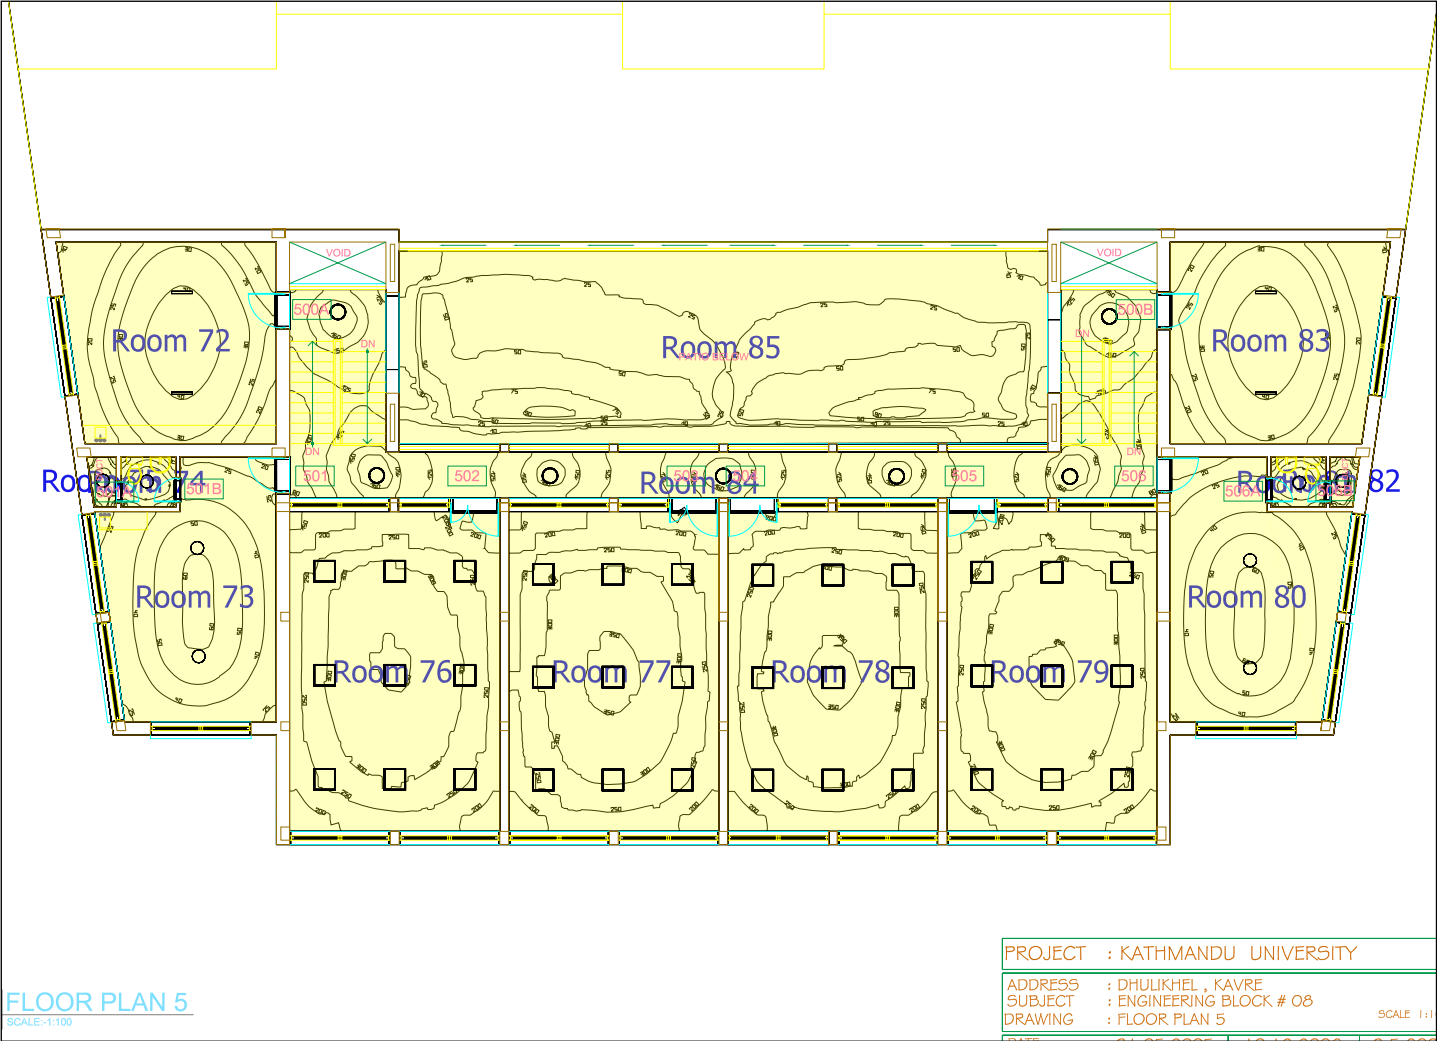


Scale: 1 : 207

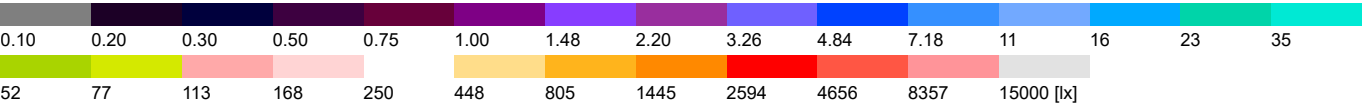


Room 1


Storey 1 , Illuminance values in [lx]

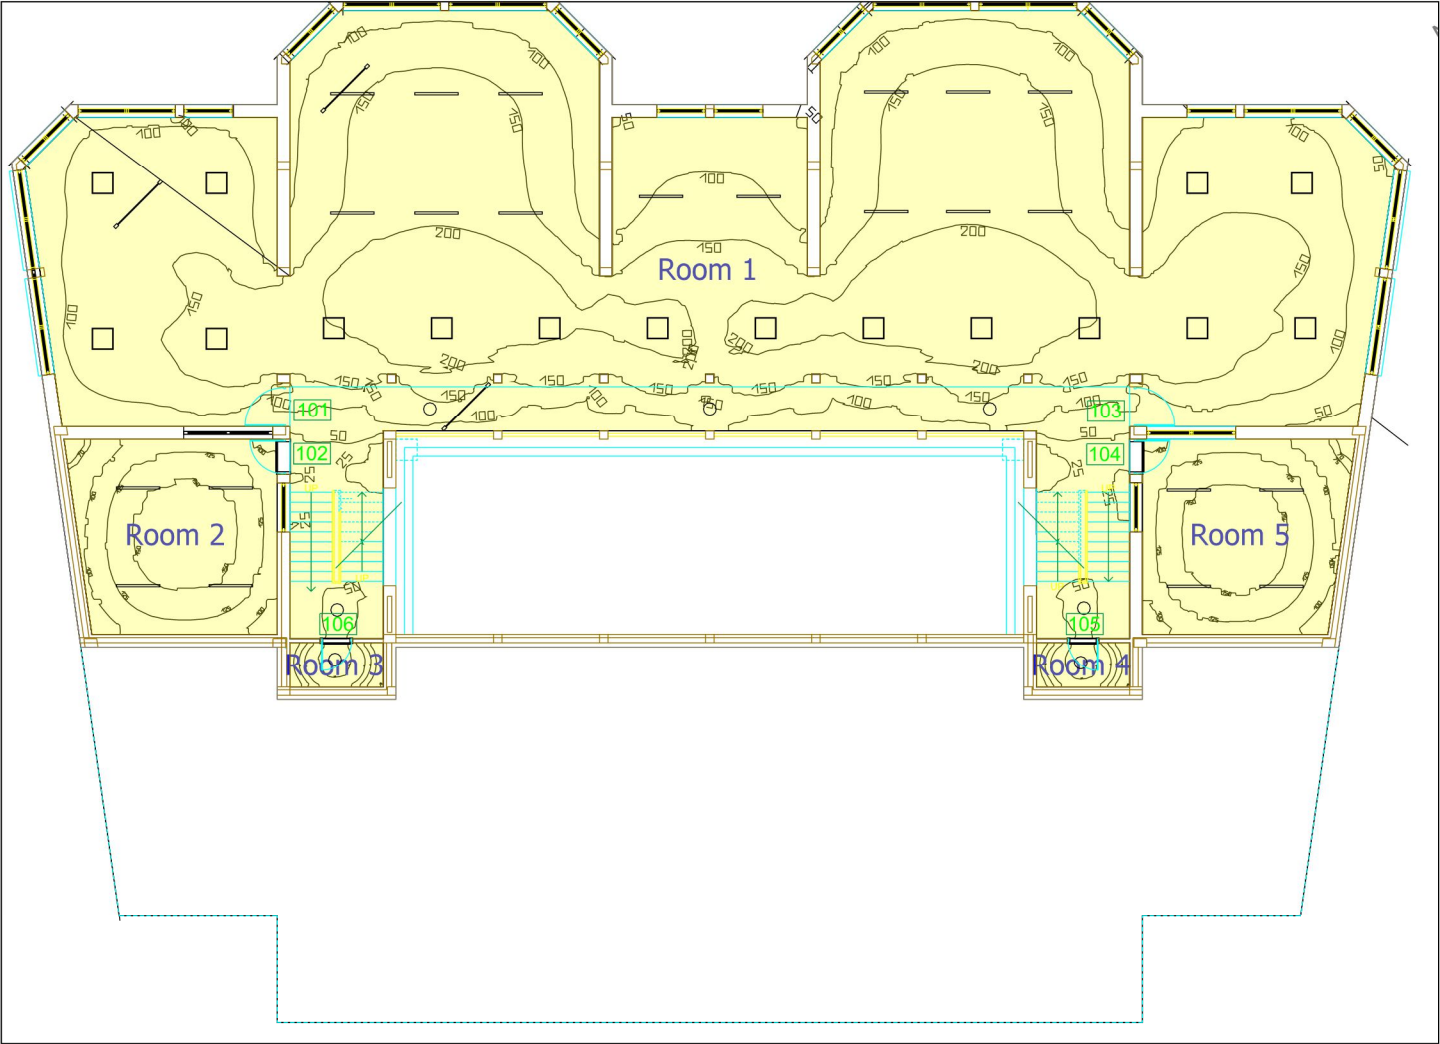


Scale: 1 : 214

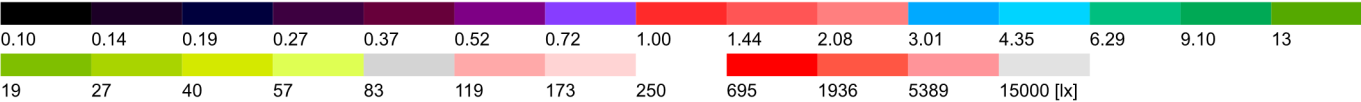


Storey 1 (3D), Illuminance values in [lx]

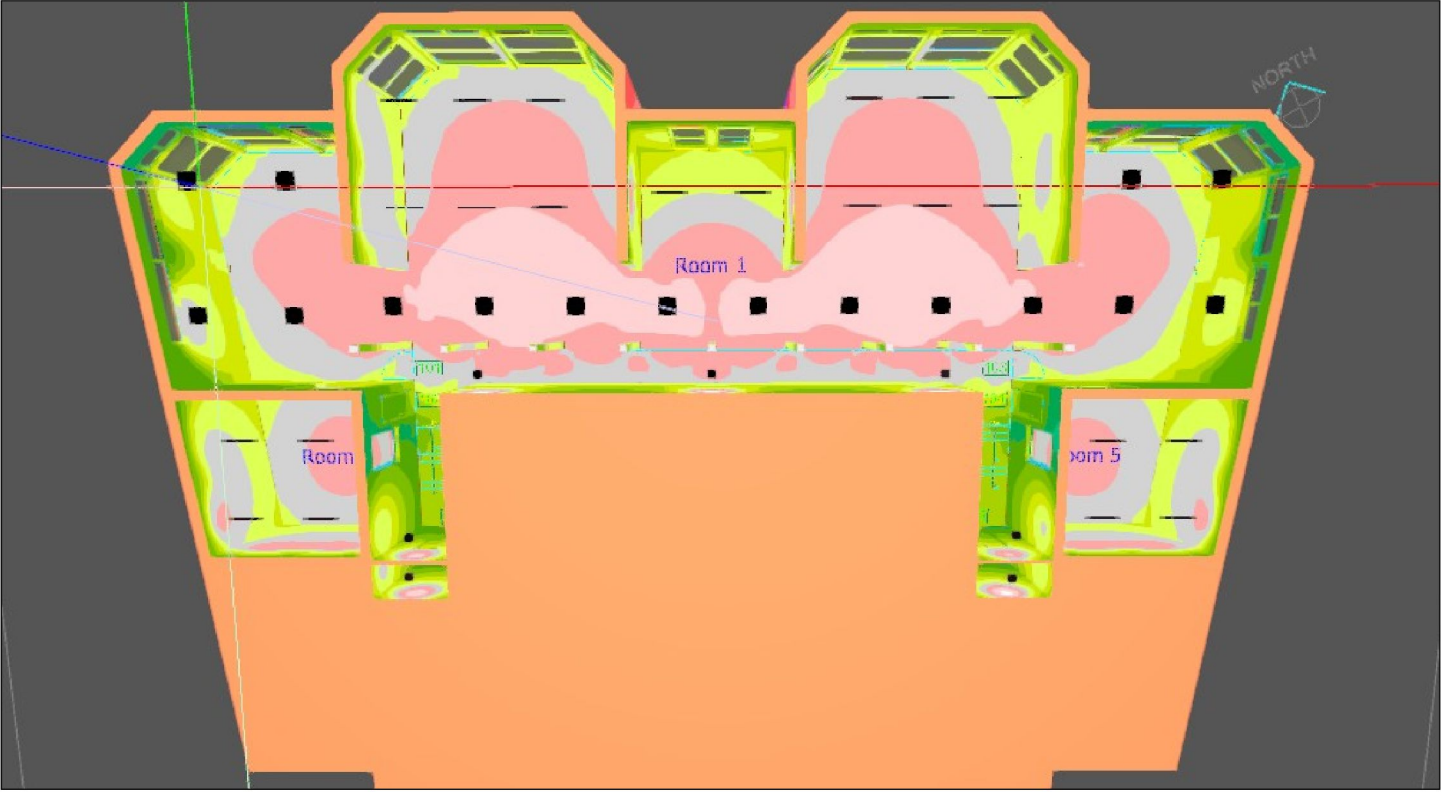


Storey 2 , Illuminance values in [lx]

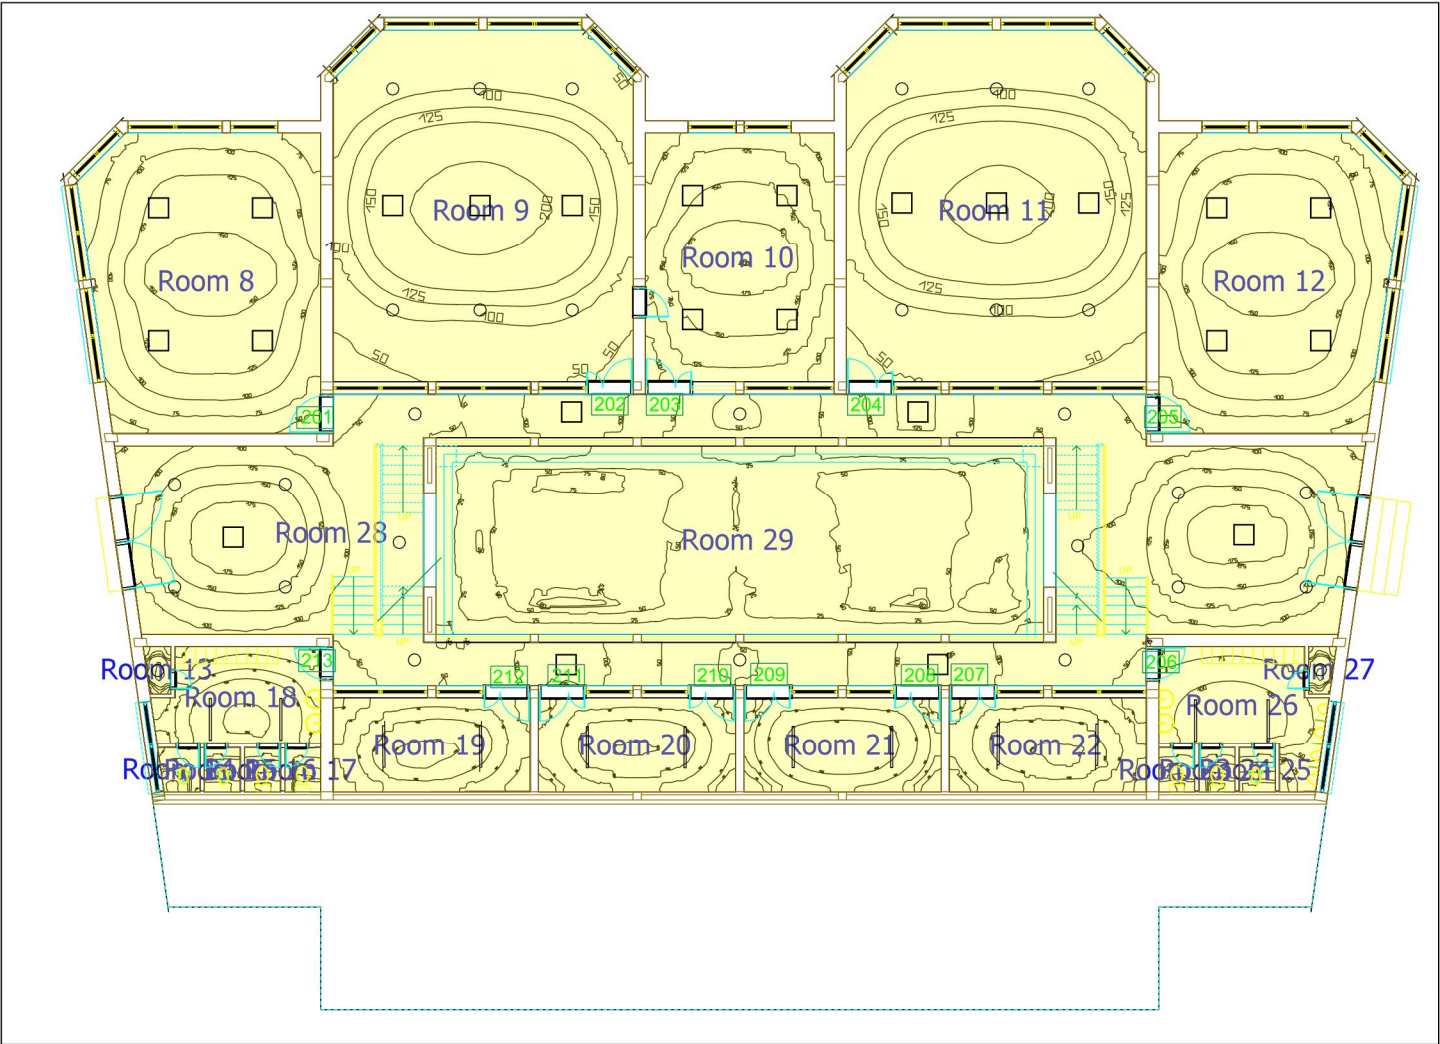


Scale: 1 : 221

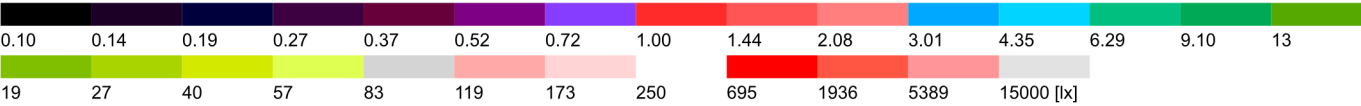

Storey 2 (3D), Illuminance values in [lx]

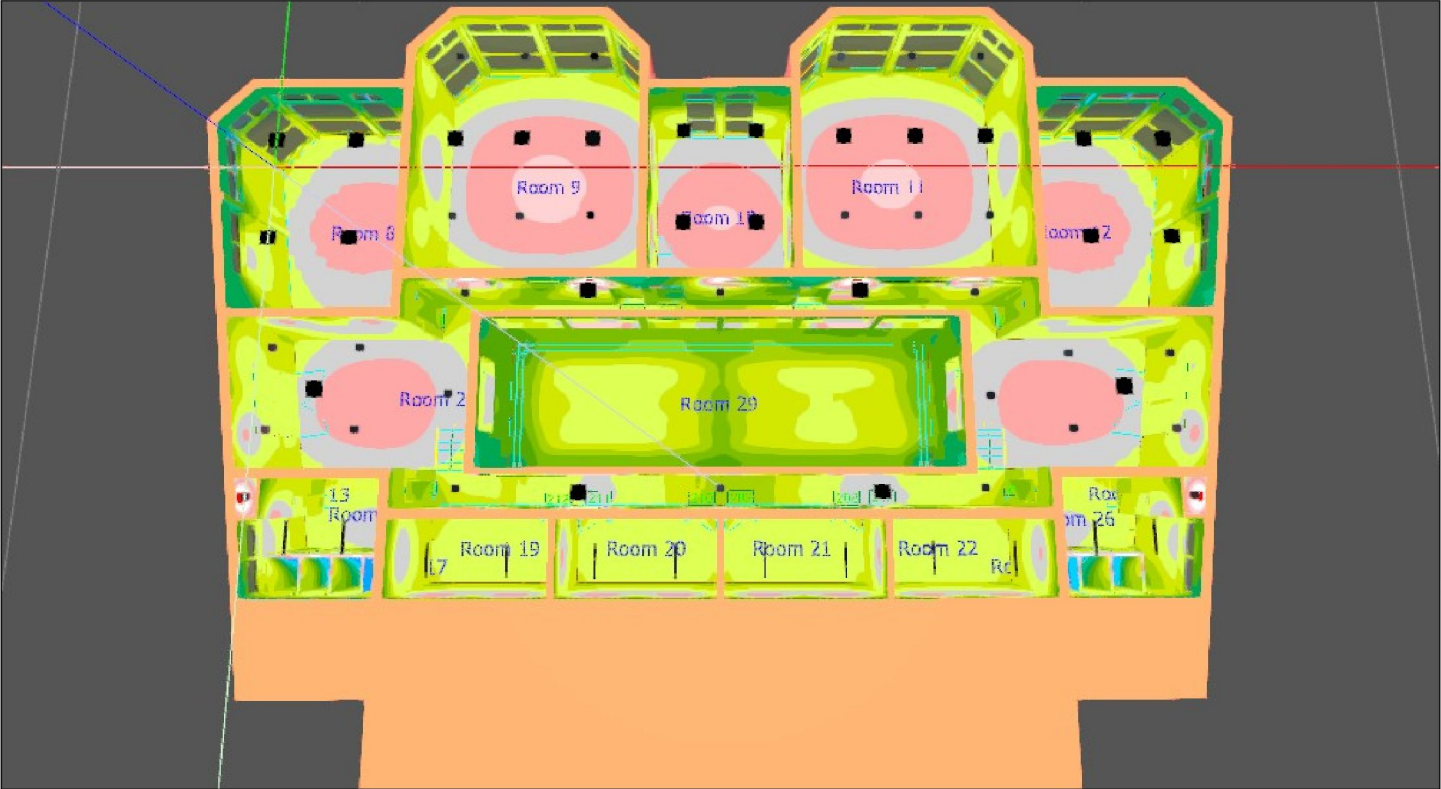


Storey 3, Illuminance values in [lx]

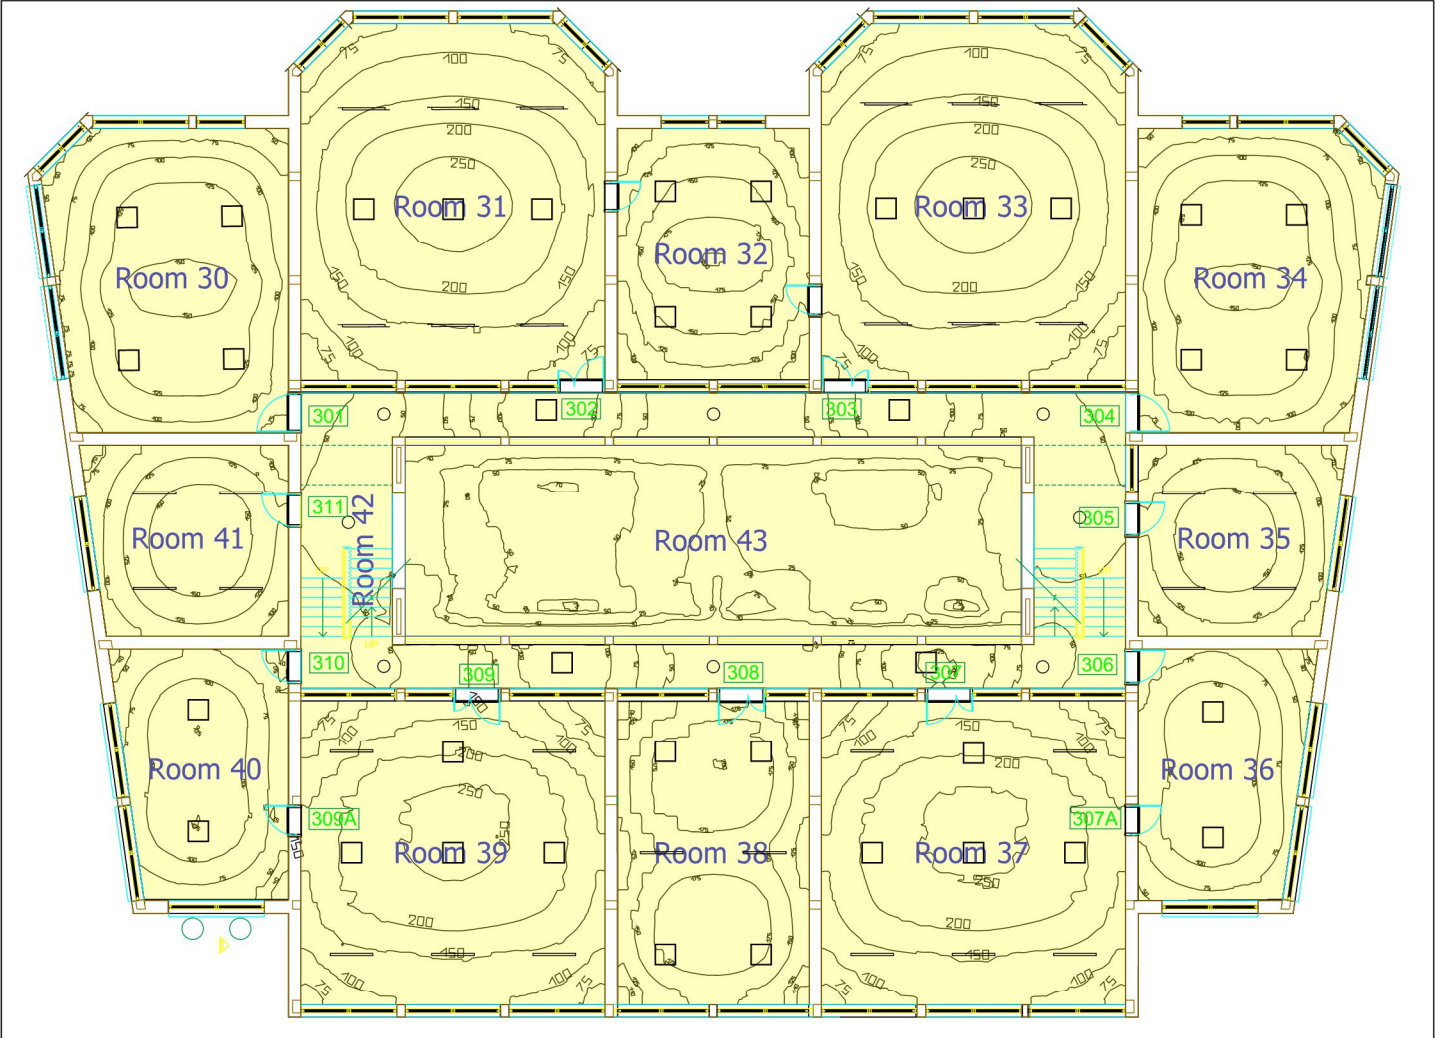


Scale: 1 : 218




Storey 3 (3D), Illuminance values in [lx]

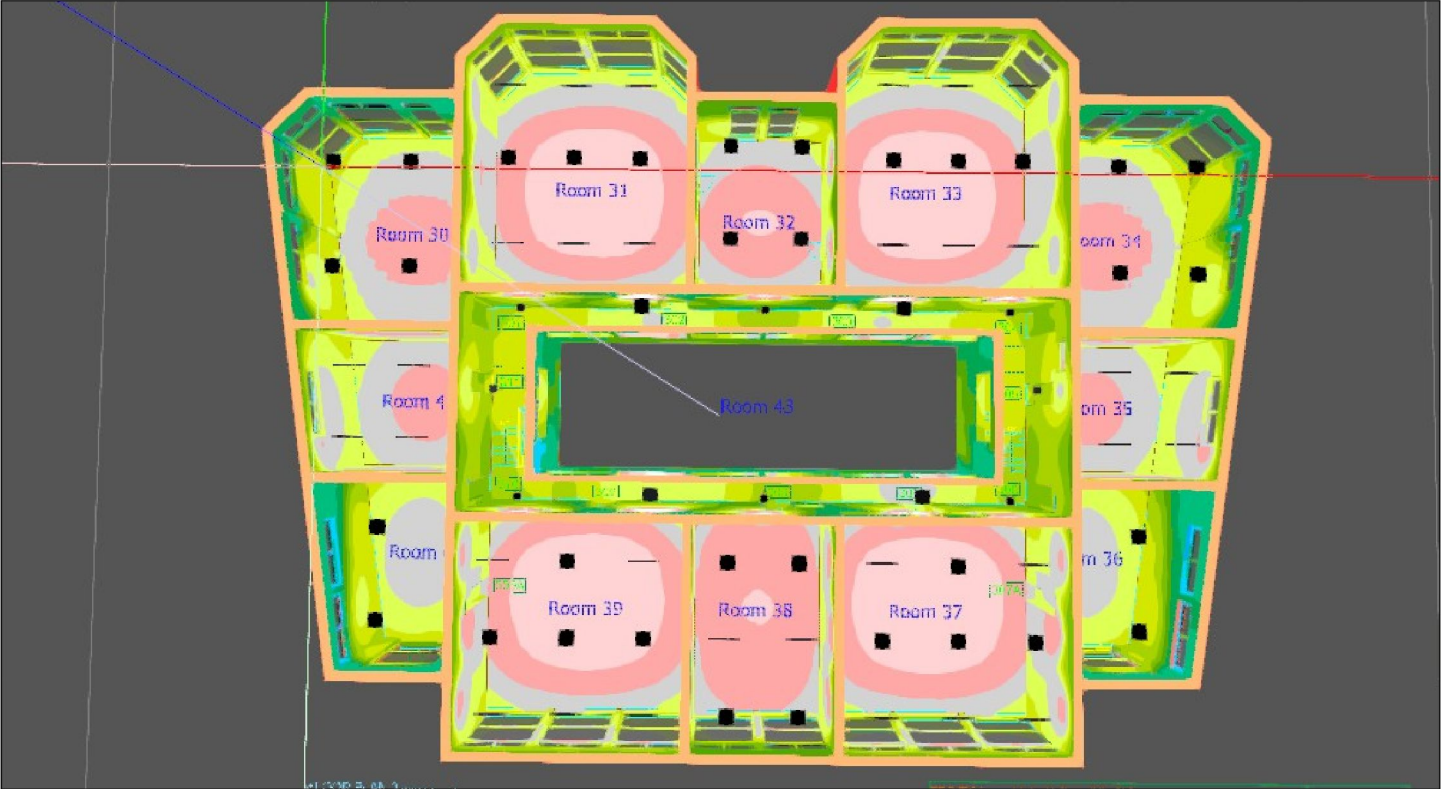


Storey 4 , Illuminance values in [lx]

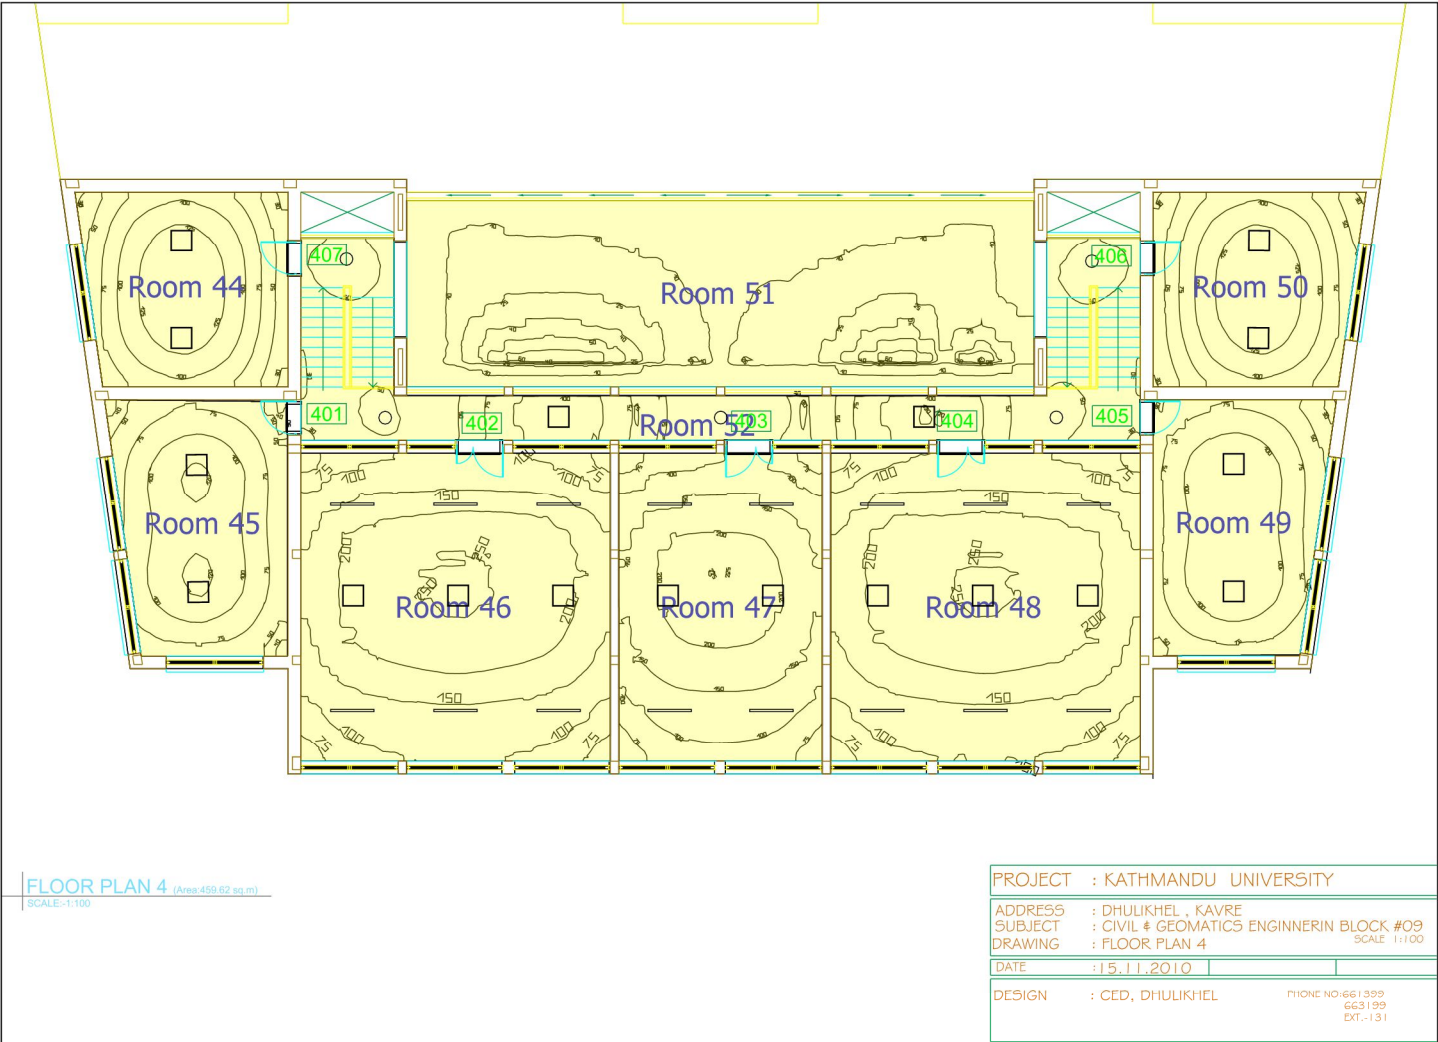


Scale: 1 : 214

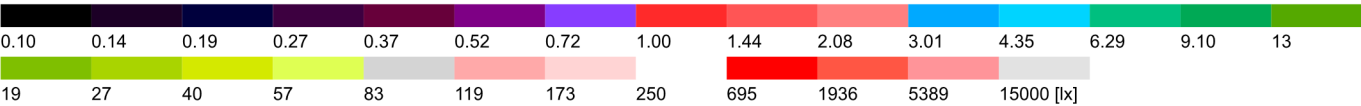


Storey 4 (3D), Illuminance values in [lx]

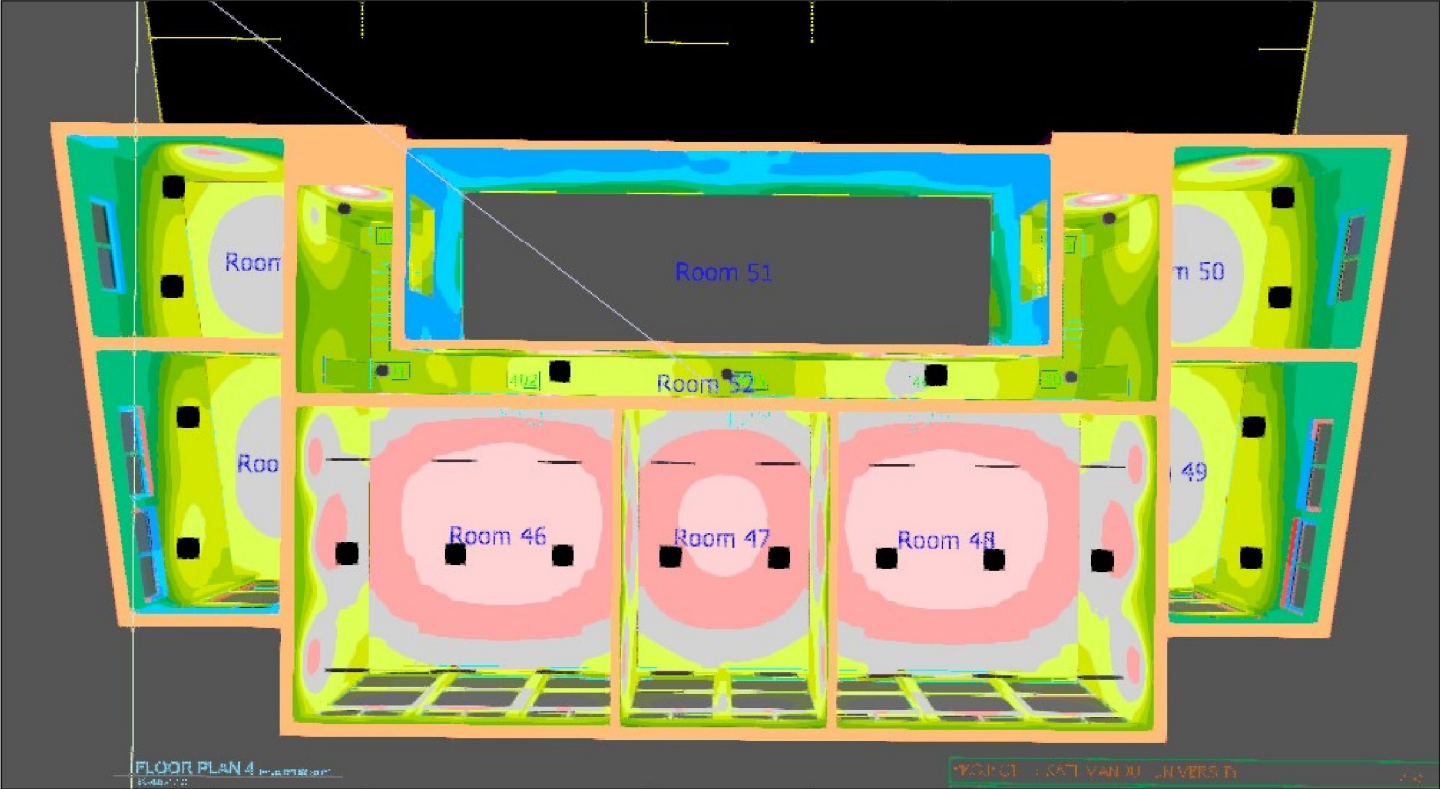


Building 1, Illuminance values in [lx]

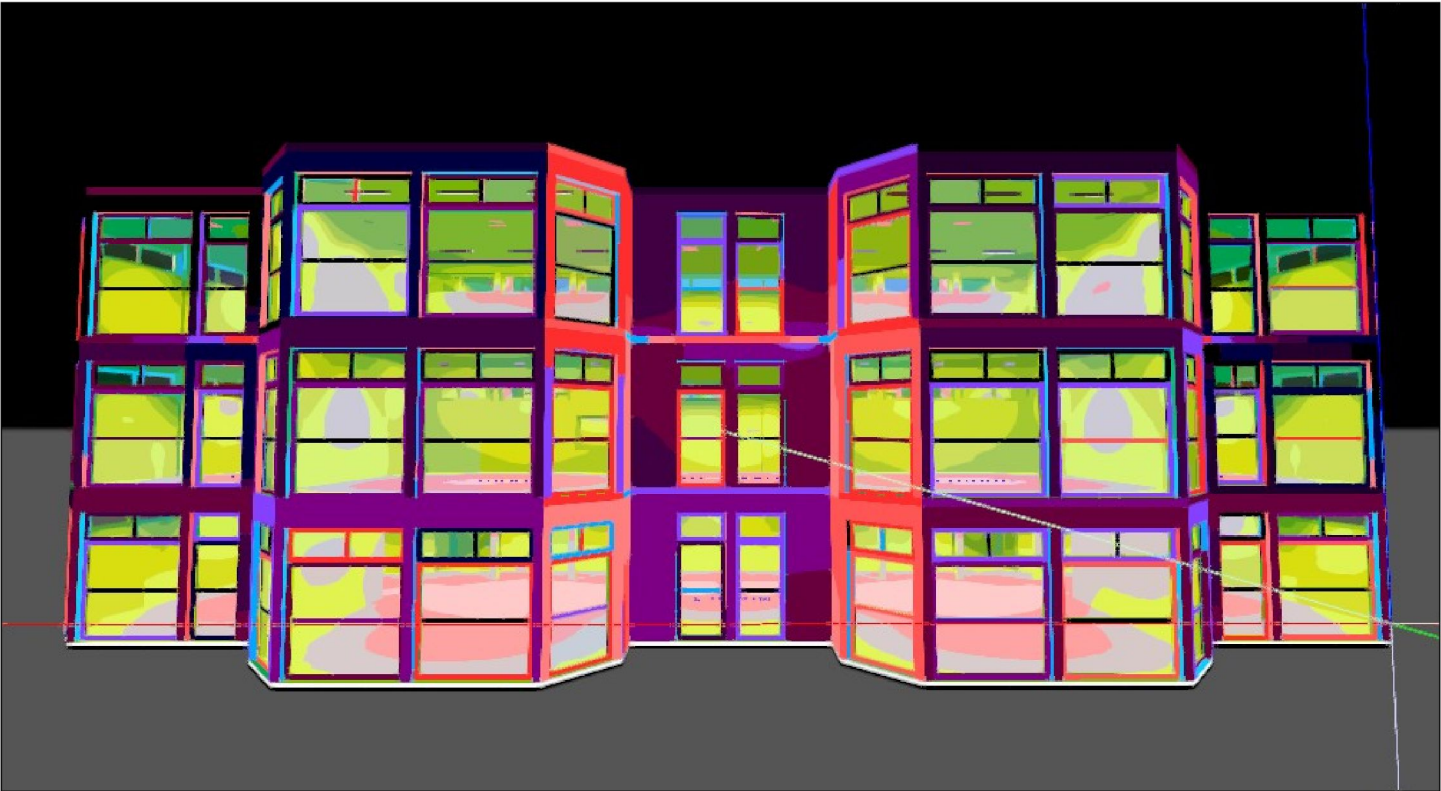


A1. Wiring Arrangement of Block 9

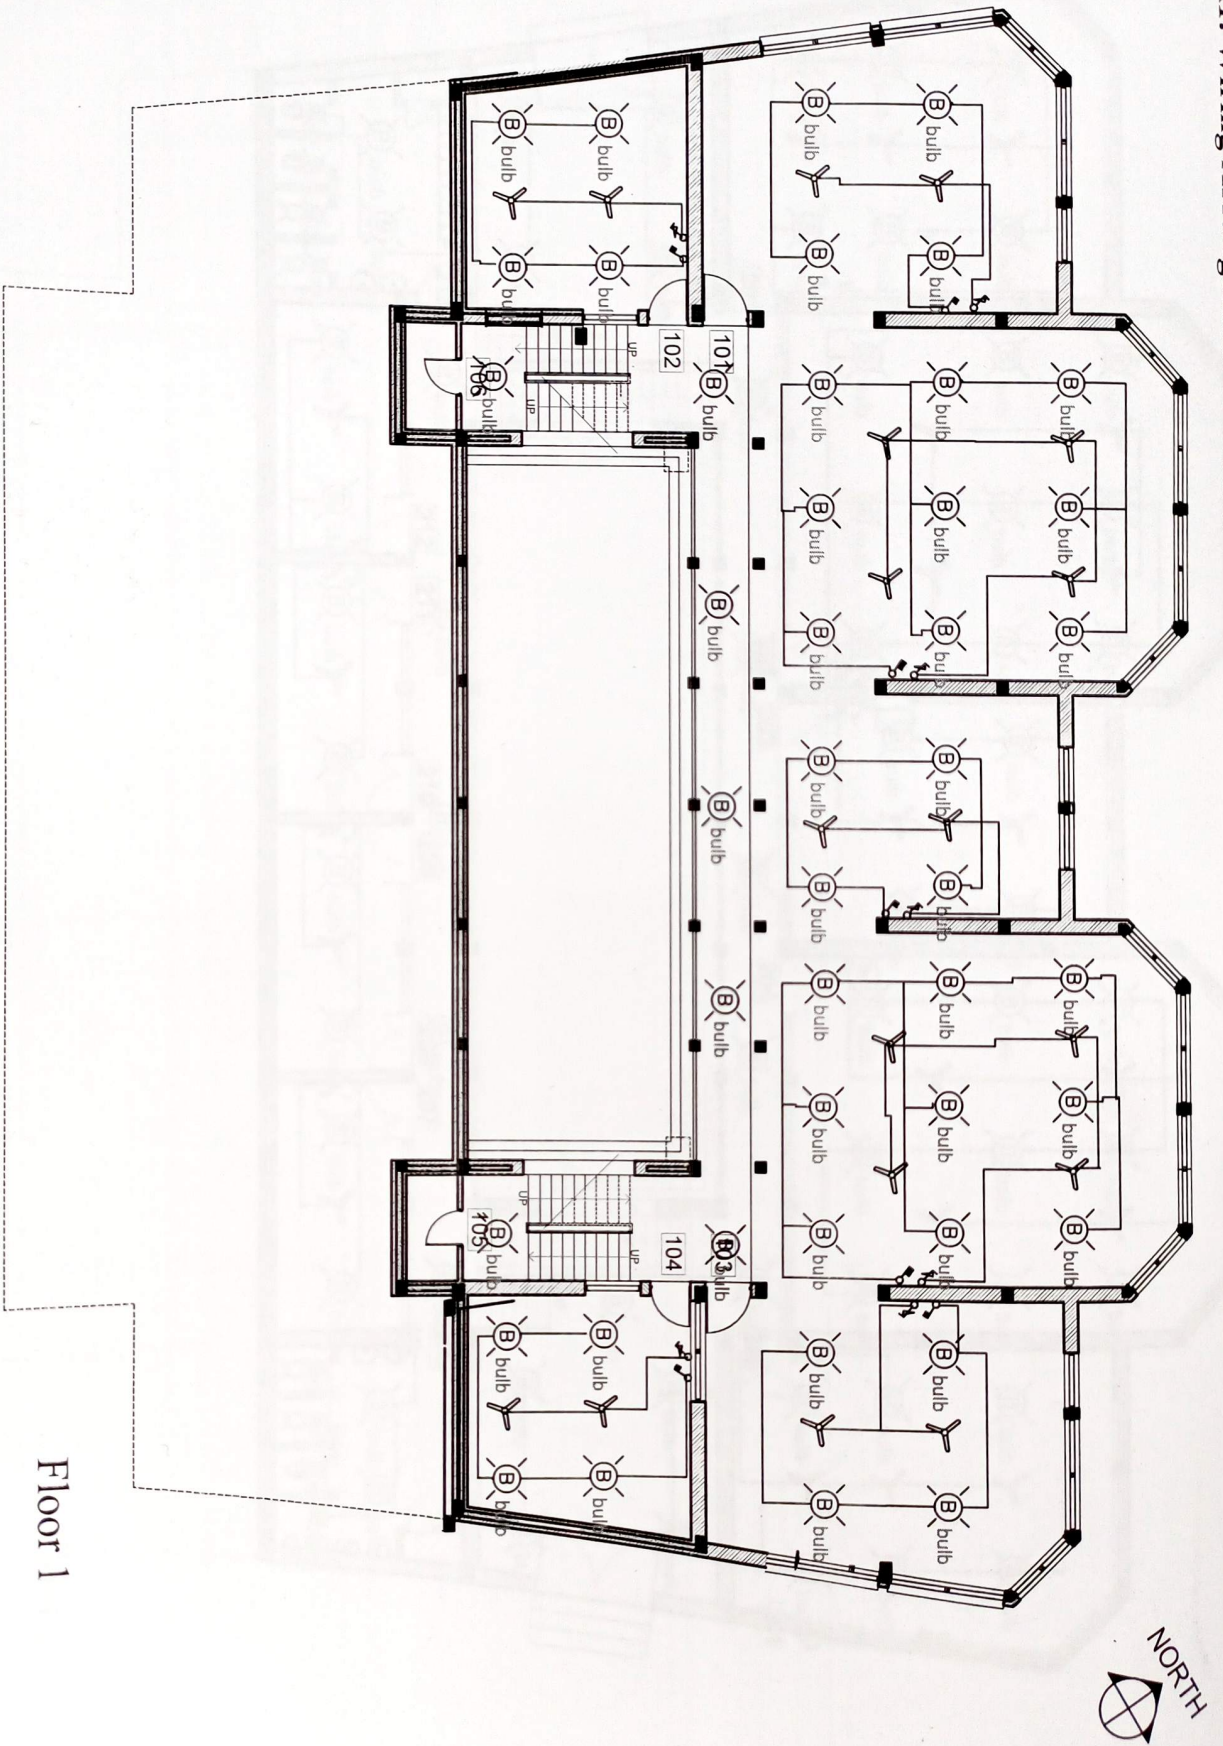


Floor 1

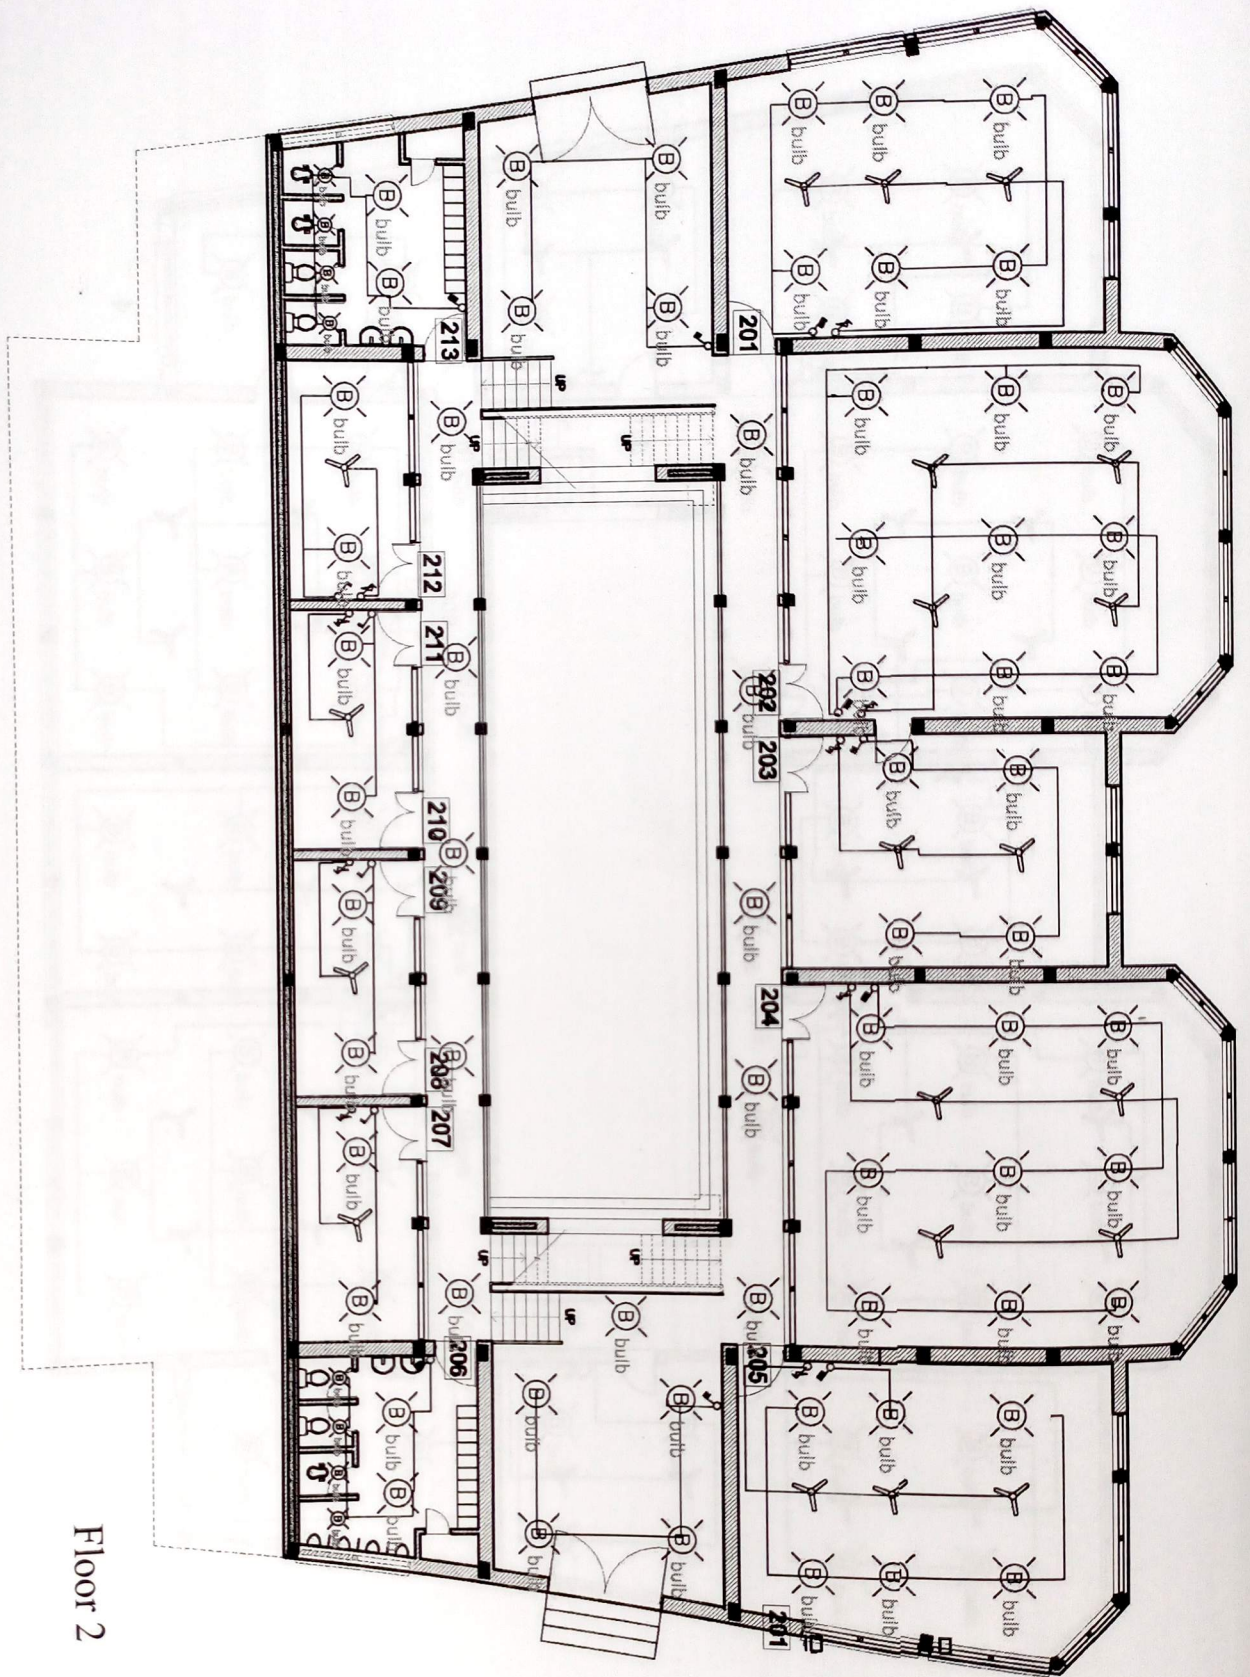

Floor 2

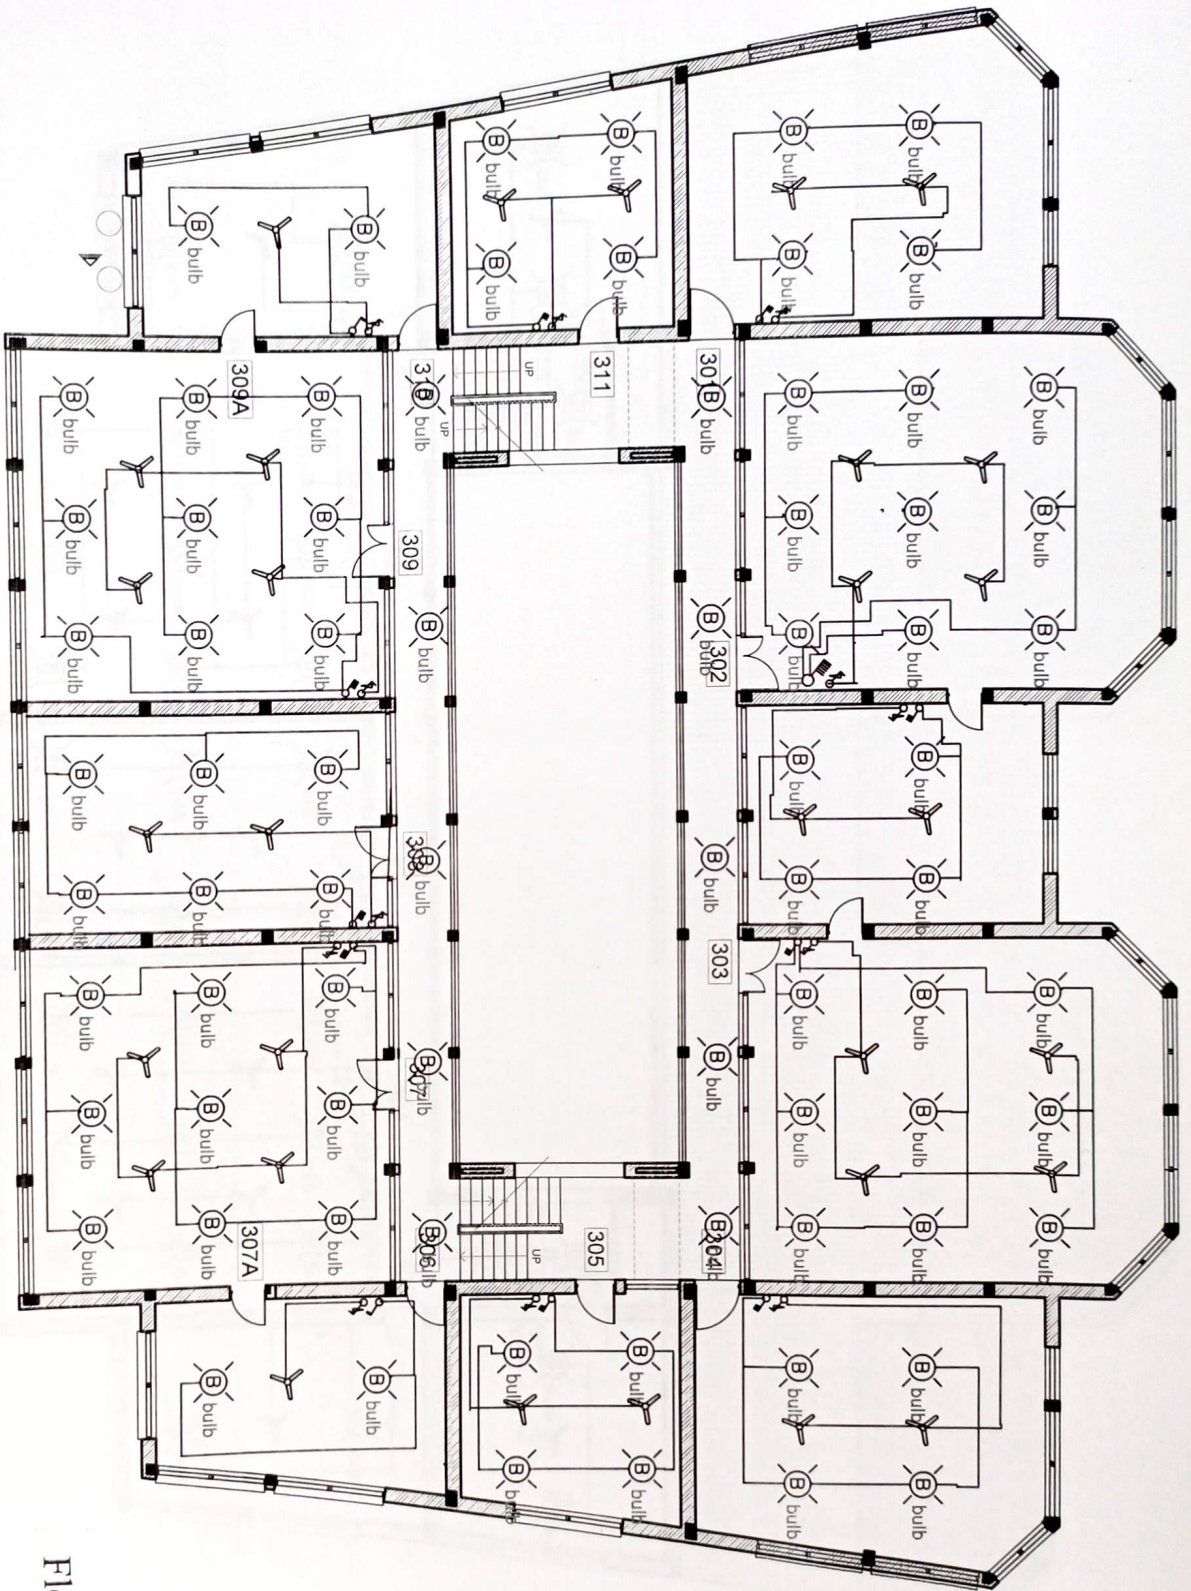

Floor 3

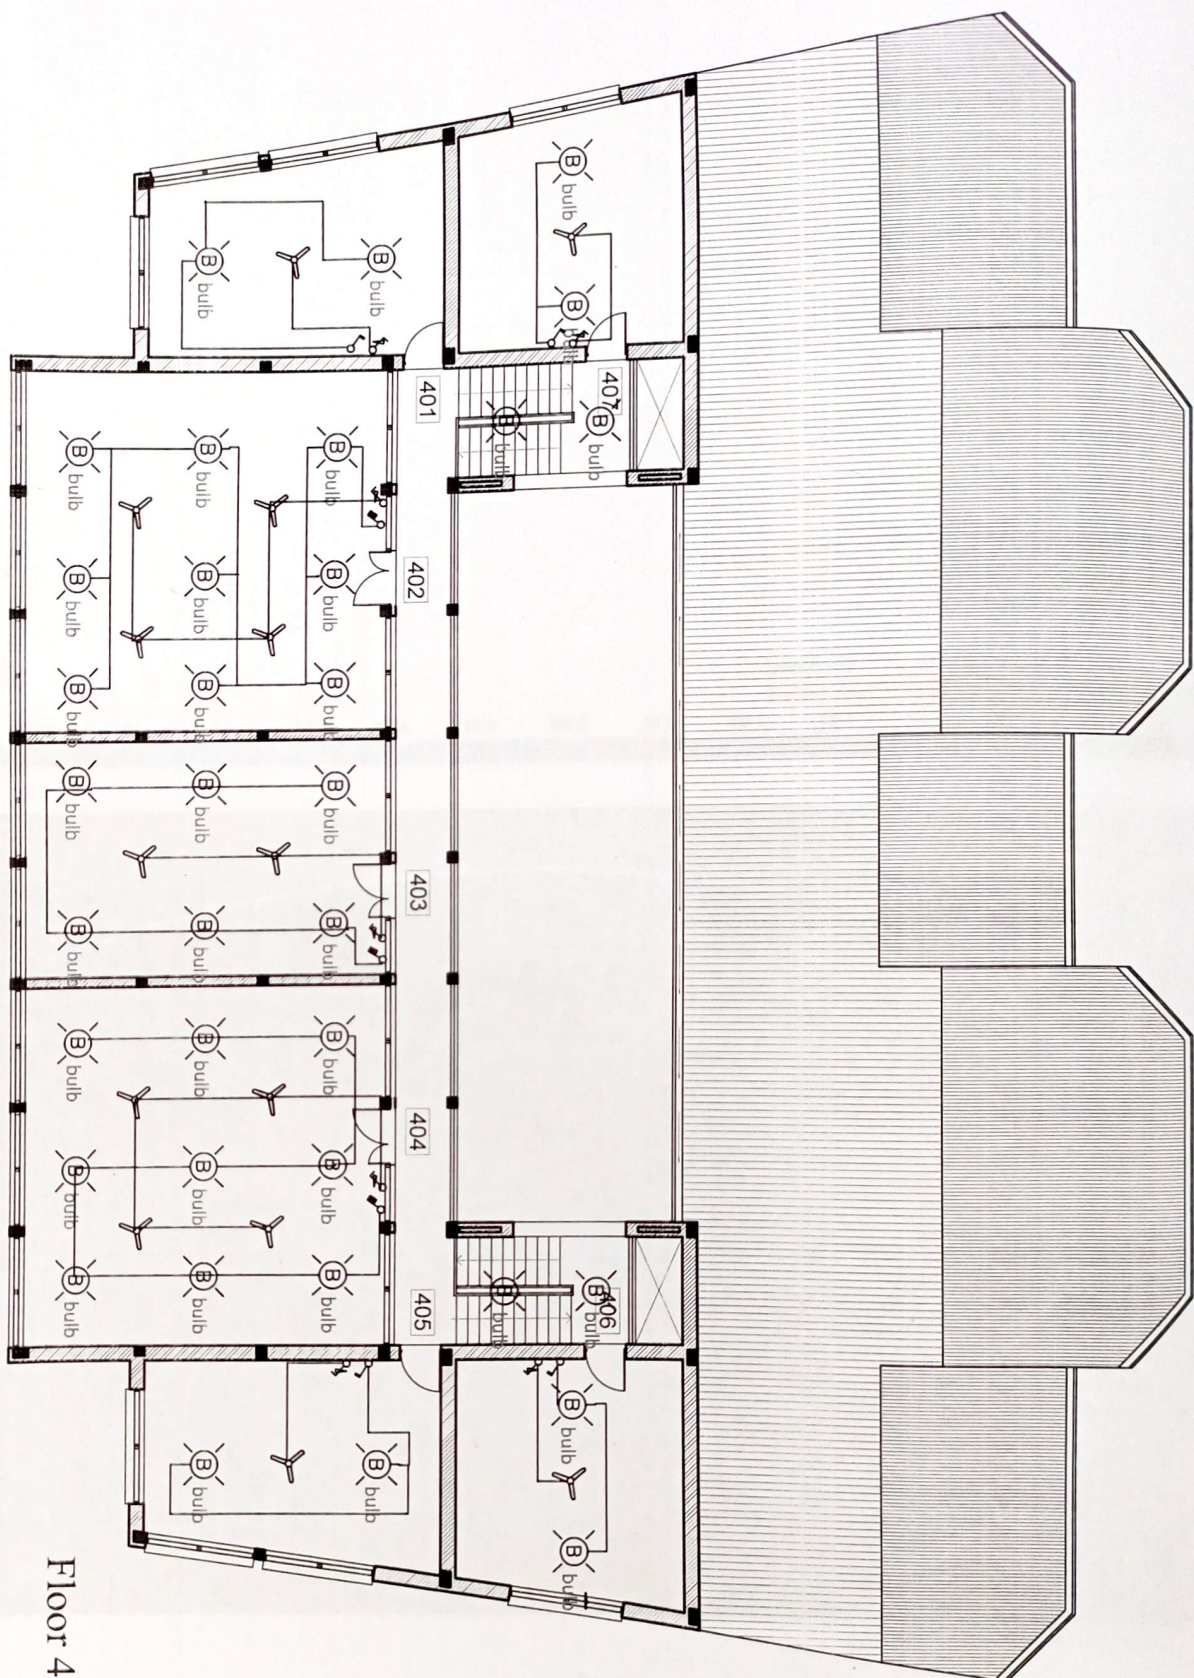

Floor 4